



SGA | SCHRAIFER
GOLDIN
ARQUITECTOS

PLANTAS


ESC. 1:250

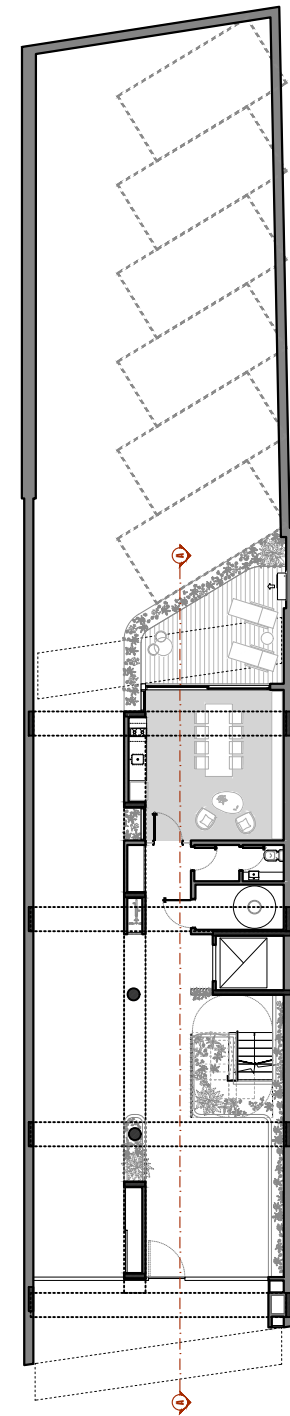

PLANTA BAJA

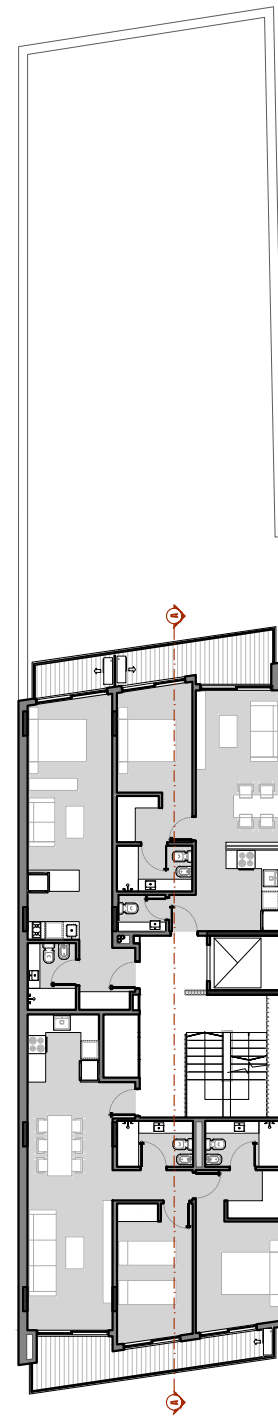


PLANTA TIPO
(2°-4°)

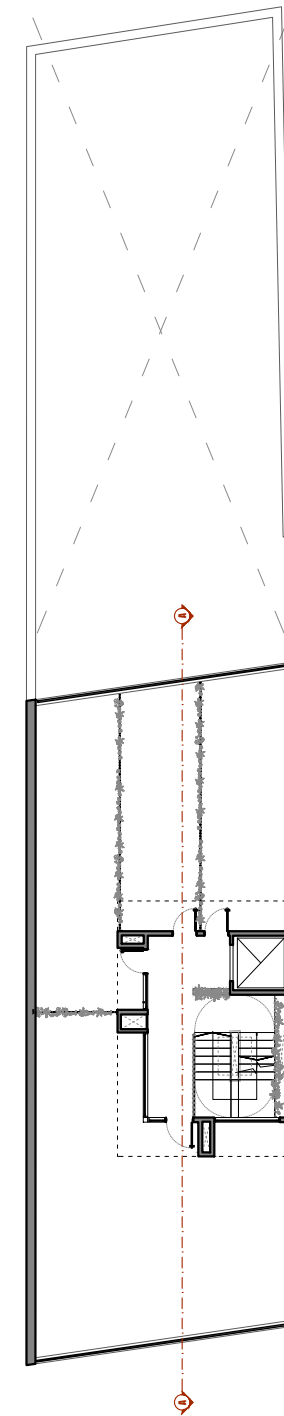

TERRAZA

PLANTA BAJA
ESC. 1:75

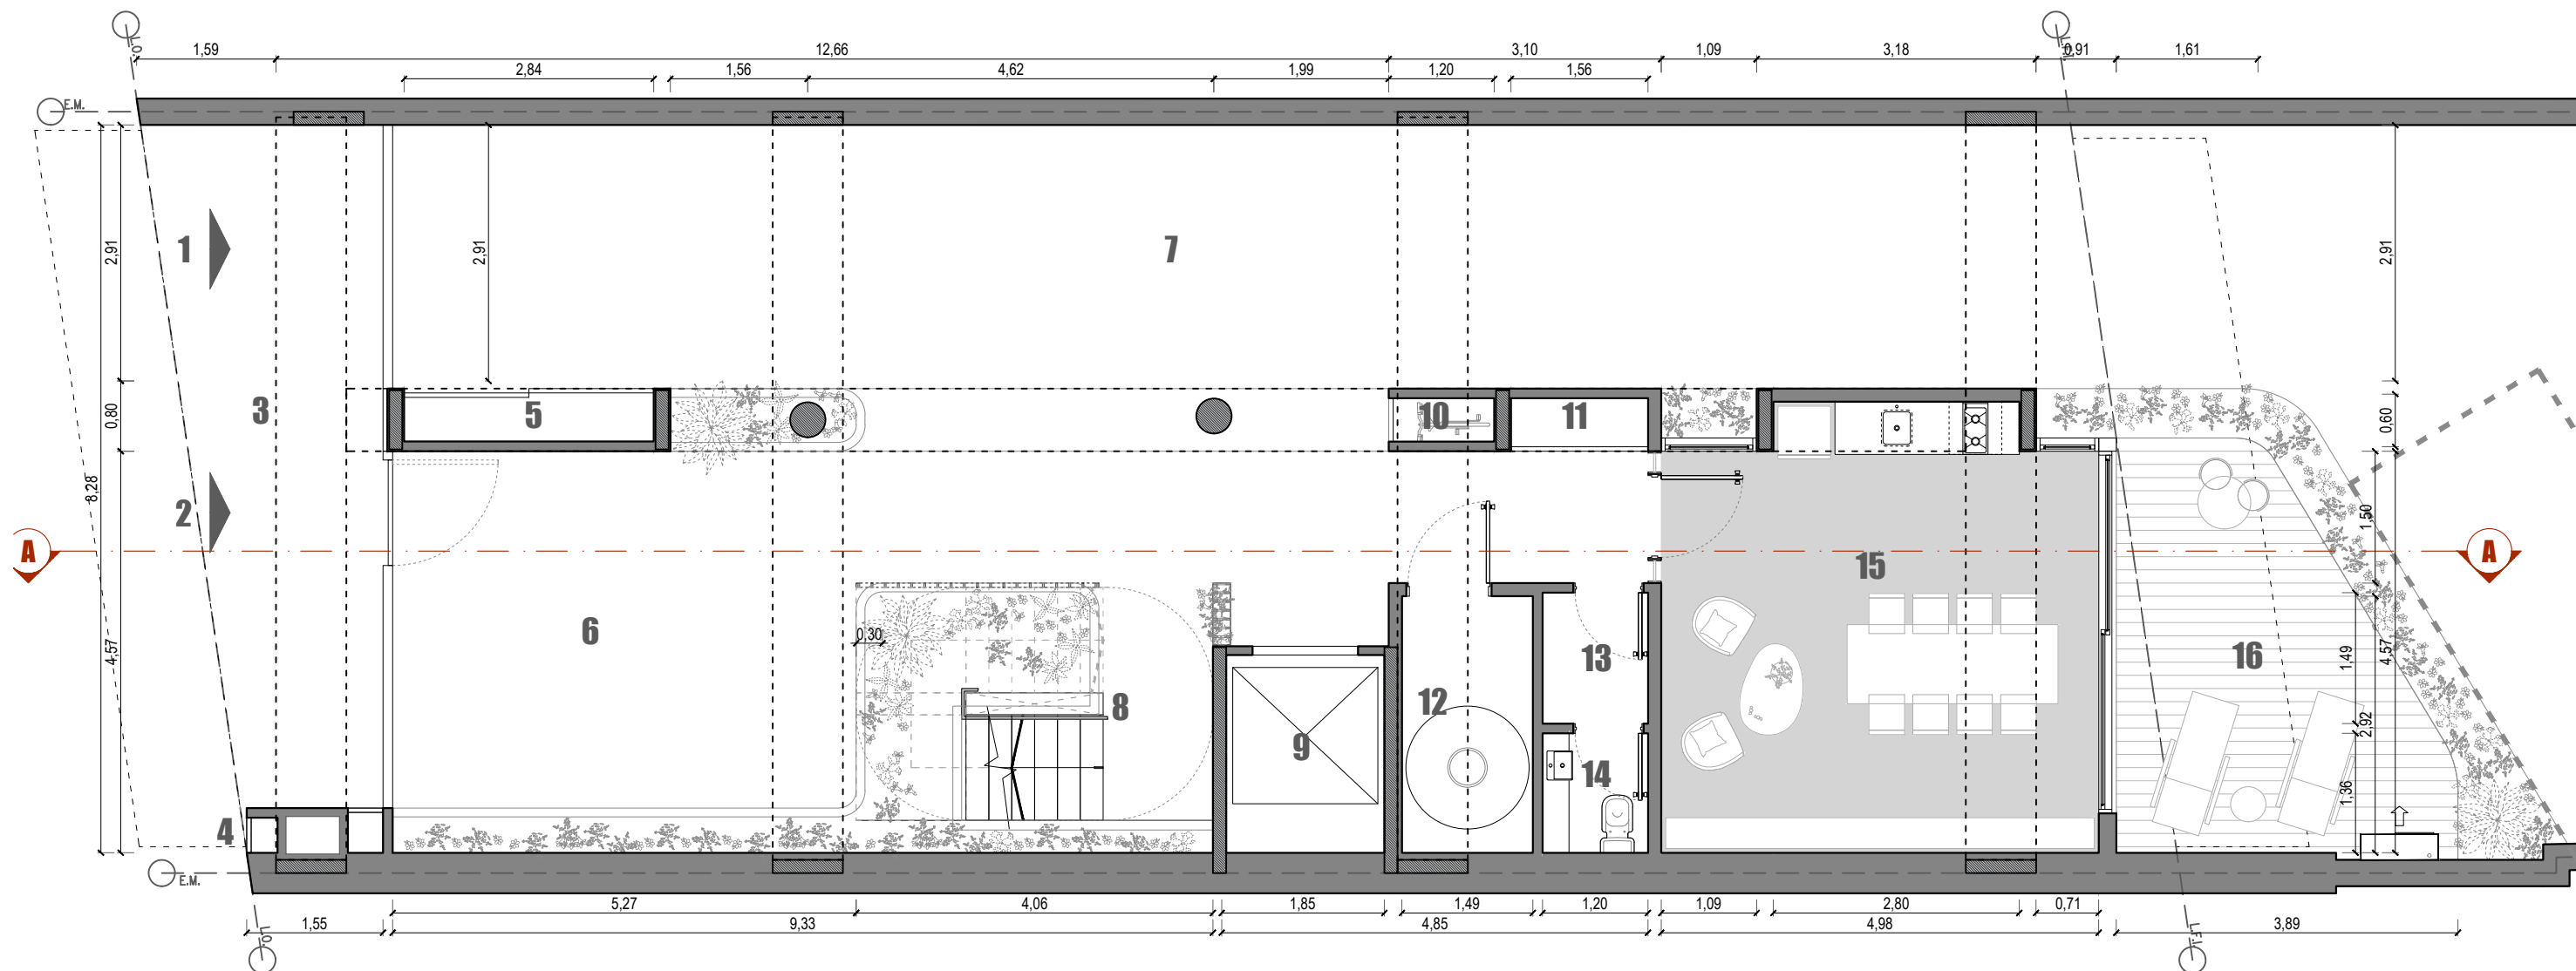

REFERENCIAS

- | | |
|---------------------|---------------------------|
| 1. ACCESO VEHÍCULAR | 7. CIRCULACIÓN VEHÍCULAR |
| 2. ACCESO PEATONAL | 8. ESCALERA |
| 3. BUZON EDESUR | 9. ASCENSOR |
| 4. NICHOS DE GAS | 10. BAULERA / BICICLETERO |
| 5. MEDIDORES | 11. GUARDADO |
| 6. HALL ACCESO | 12. SALA DE BOMBEO |


- | |
|-----------------------|
| 13. AUXILIAR PORTERÍA |
| 14. BAÑO |
| 15. SUM |
| 16. EXPANSIÓN SUM |

SUPERFICIES

- CUBIERTAS: 69.17 m²
- SEMICUBIERTAS: 4.32 m²
- DESCUBIERTAS: 157.62 m² (6 ESPACIOS)
- HALL DE ACCESO: 79.90 m²

PLANTA TIPO (2°-4°)

ESC. 1:75

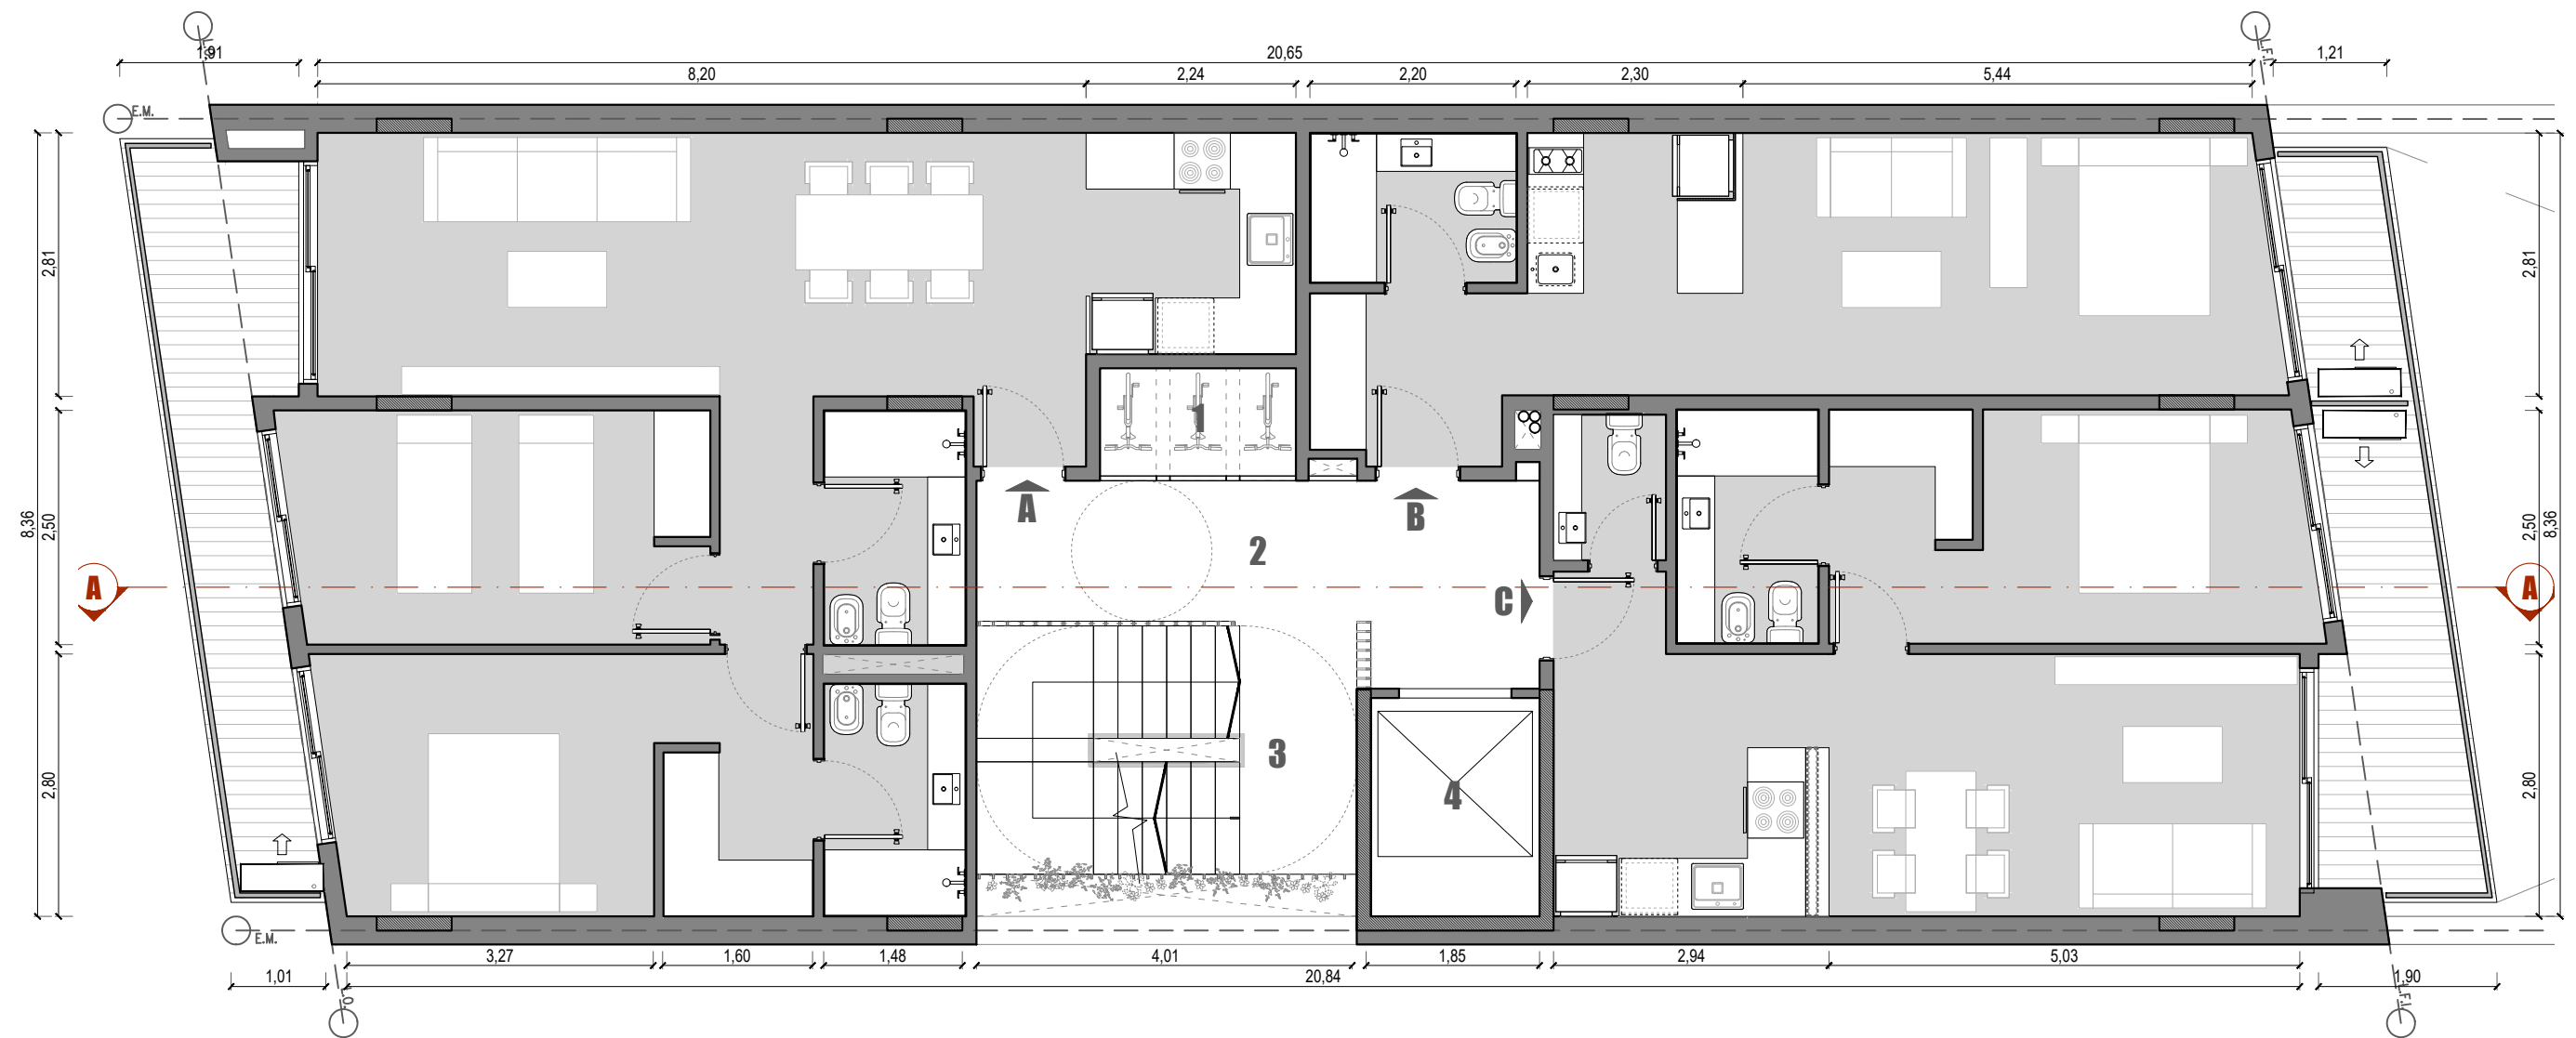


REFERENCIAS

1. BAULERAS / BICICLETEROS
2. PALIER
3. ESCALERA
4. ASCENSOR

SUPERFICIES

- UNIDAD A: 72,72m² cub. / 9,95m² semi.
- UNIDAD B: 33,25m² cub. / 3,32m² semi.
- UNIDAD C: 46,56m² cub. / 7,68m² semi.
- CIRCULACIONES: 31,92m²
- BAULERAS: 2,86m²

PLANTA TERRAZAS
ESC. 1:75

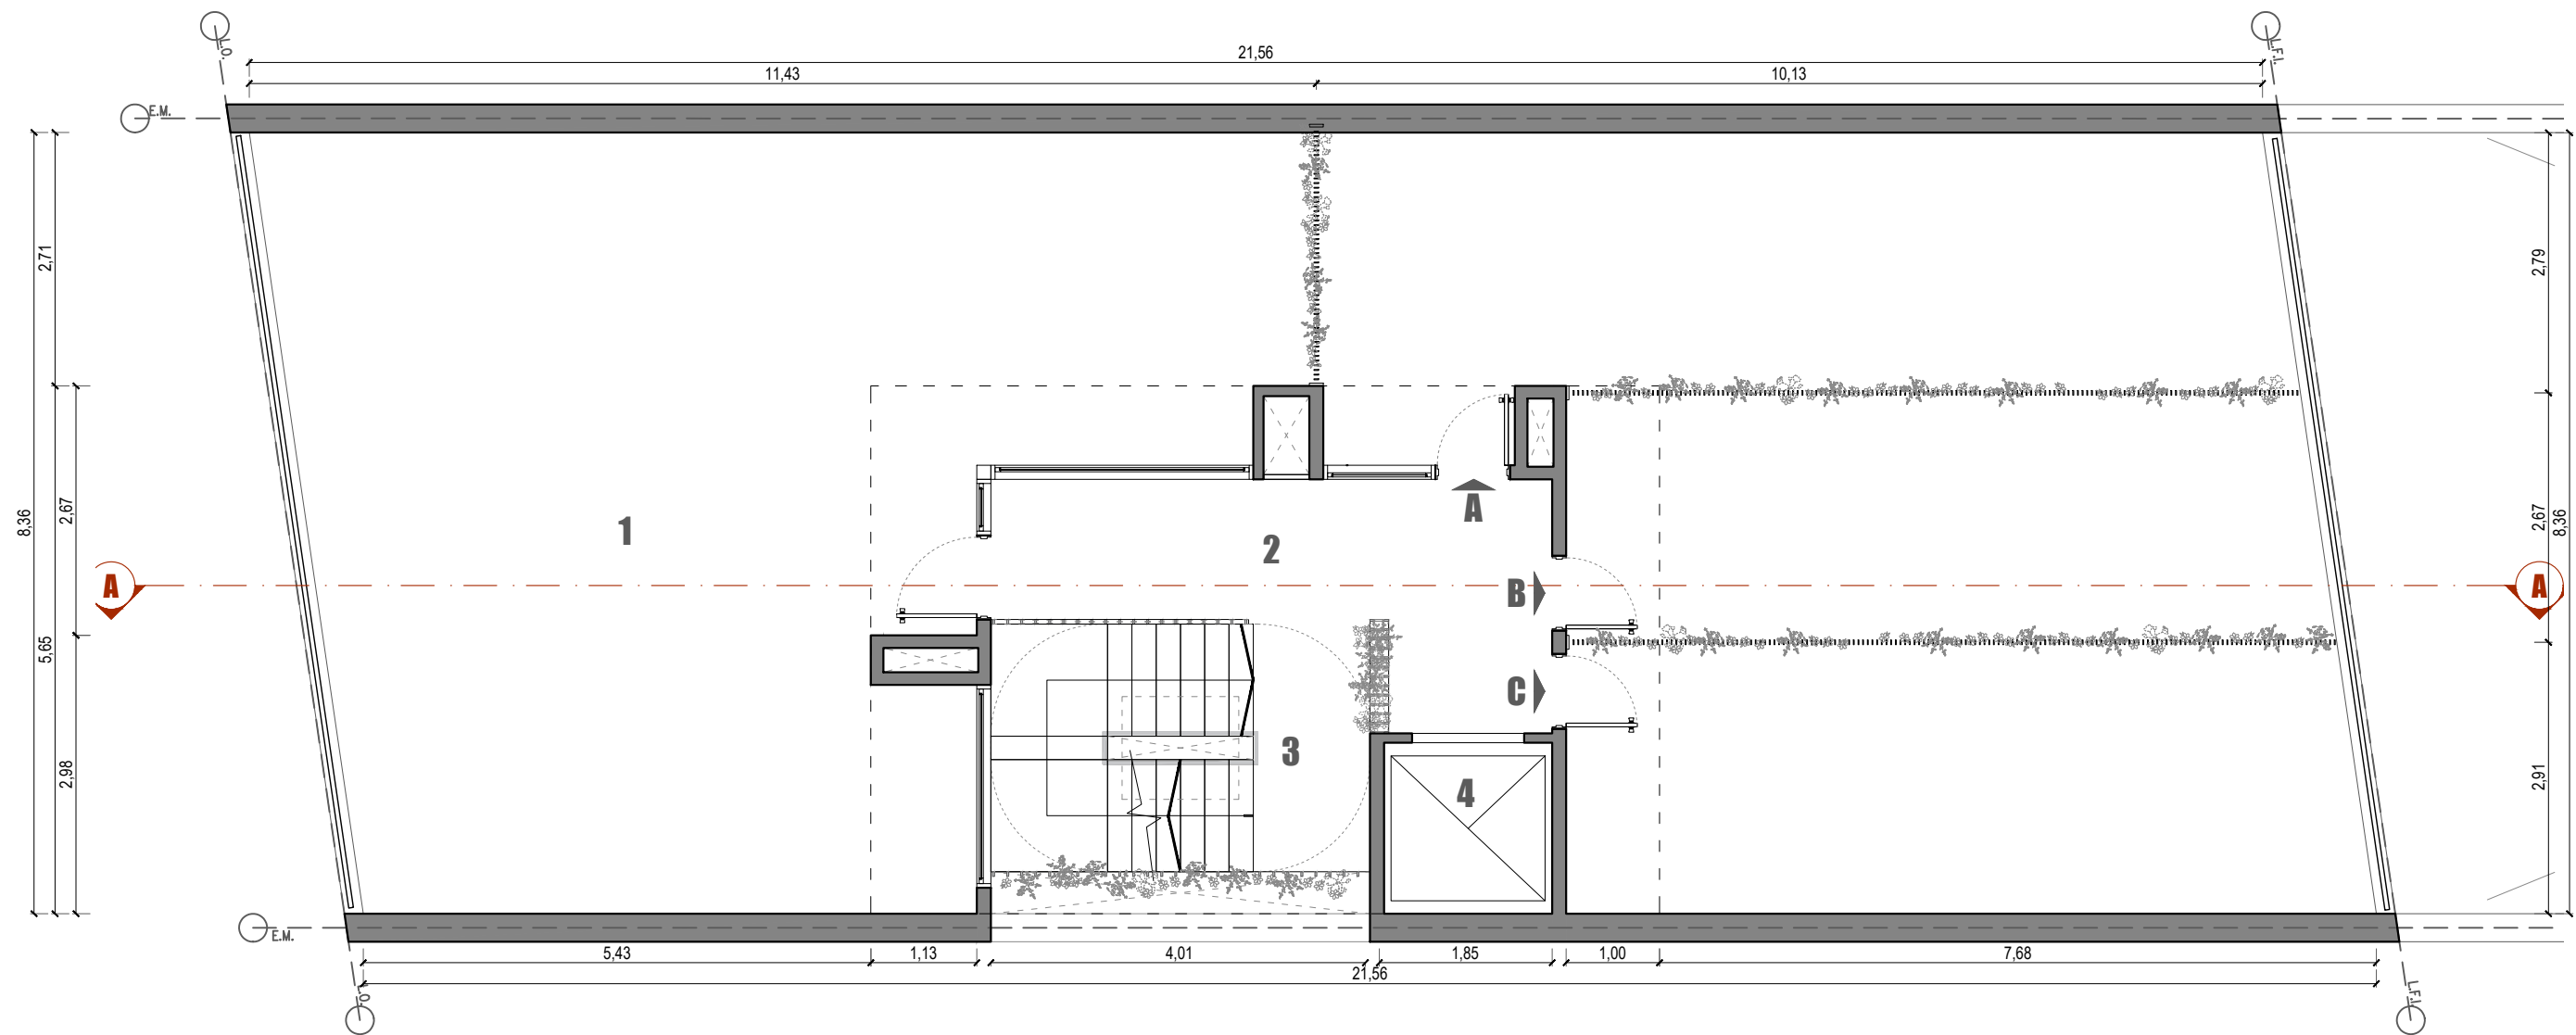

REFERENCIAS

- 1. TERRAZA DE USO COMÚN
- 2. PALIER
- 3. ESCALERA
- 4. ASCENSOR


- A. TERRAZA PRIVADA A
- B. TERRAZA PRIVADA B
- C. TERRAZA PRIVADA D

SUPERFICIES

- TERRAZA COMÚN: 76,26m²
- TERRAZA A: 42,44m²
- TERRAZA B: 22,05m²
- TERRAZA C: 26,51m²
- CIRCULACIONES: 32,94m²

CORTE

ESC. 1:75

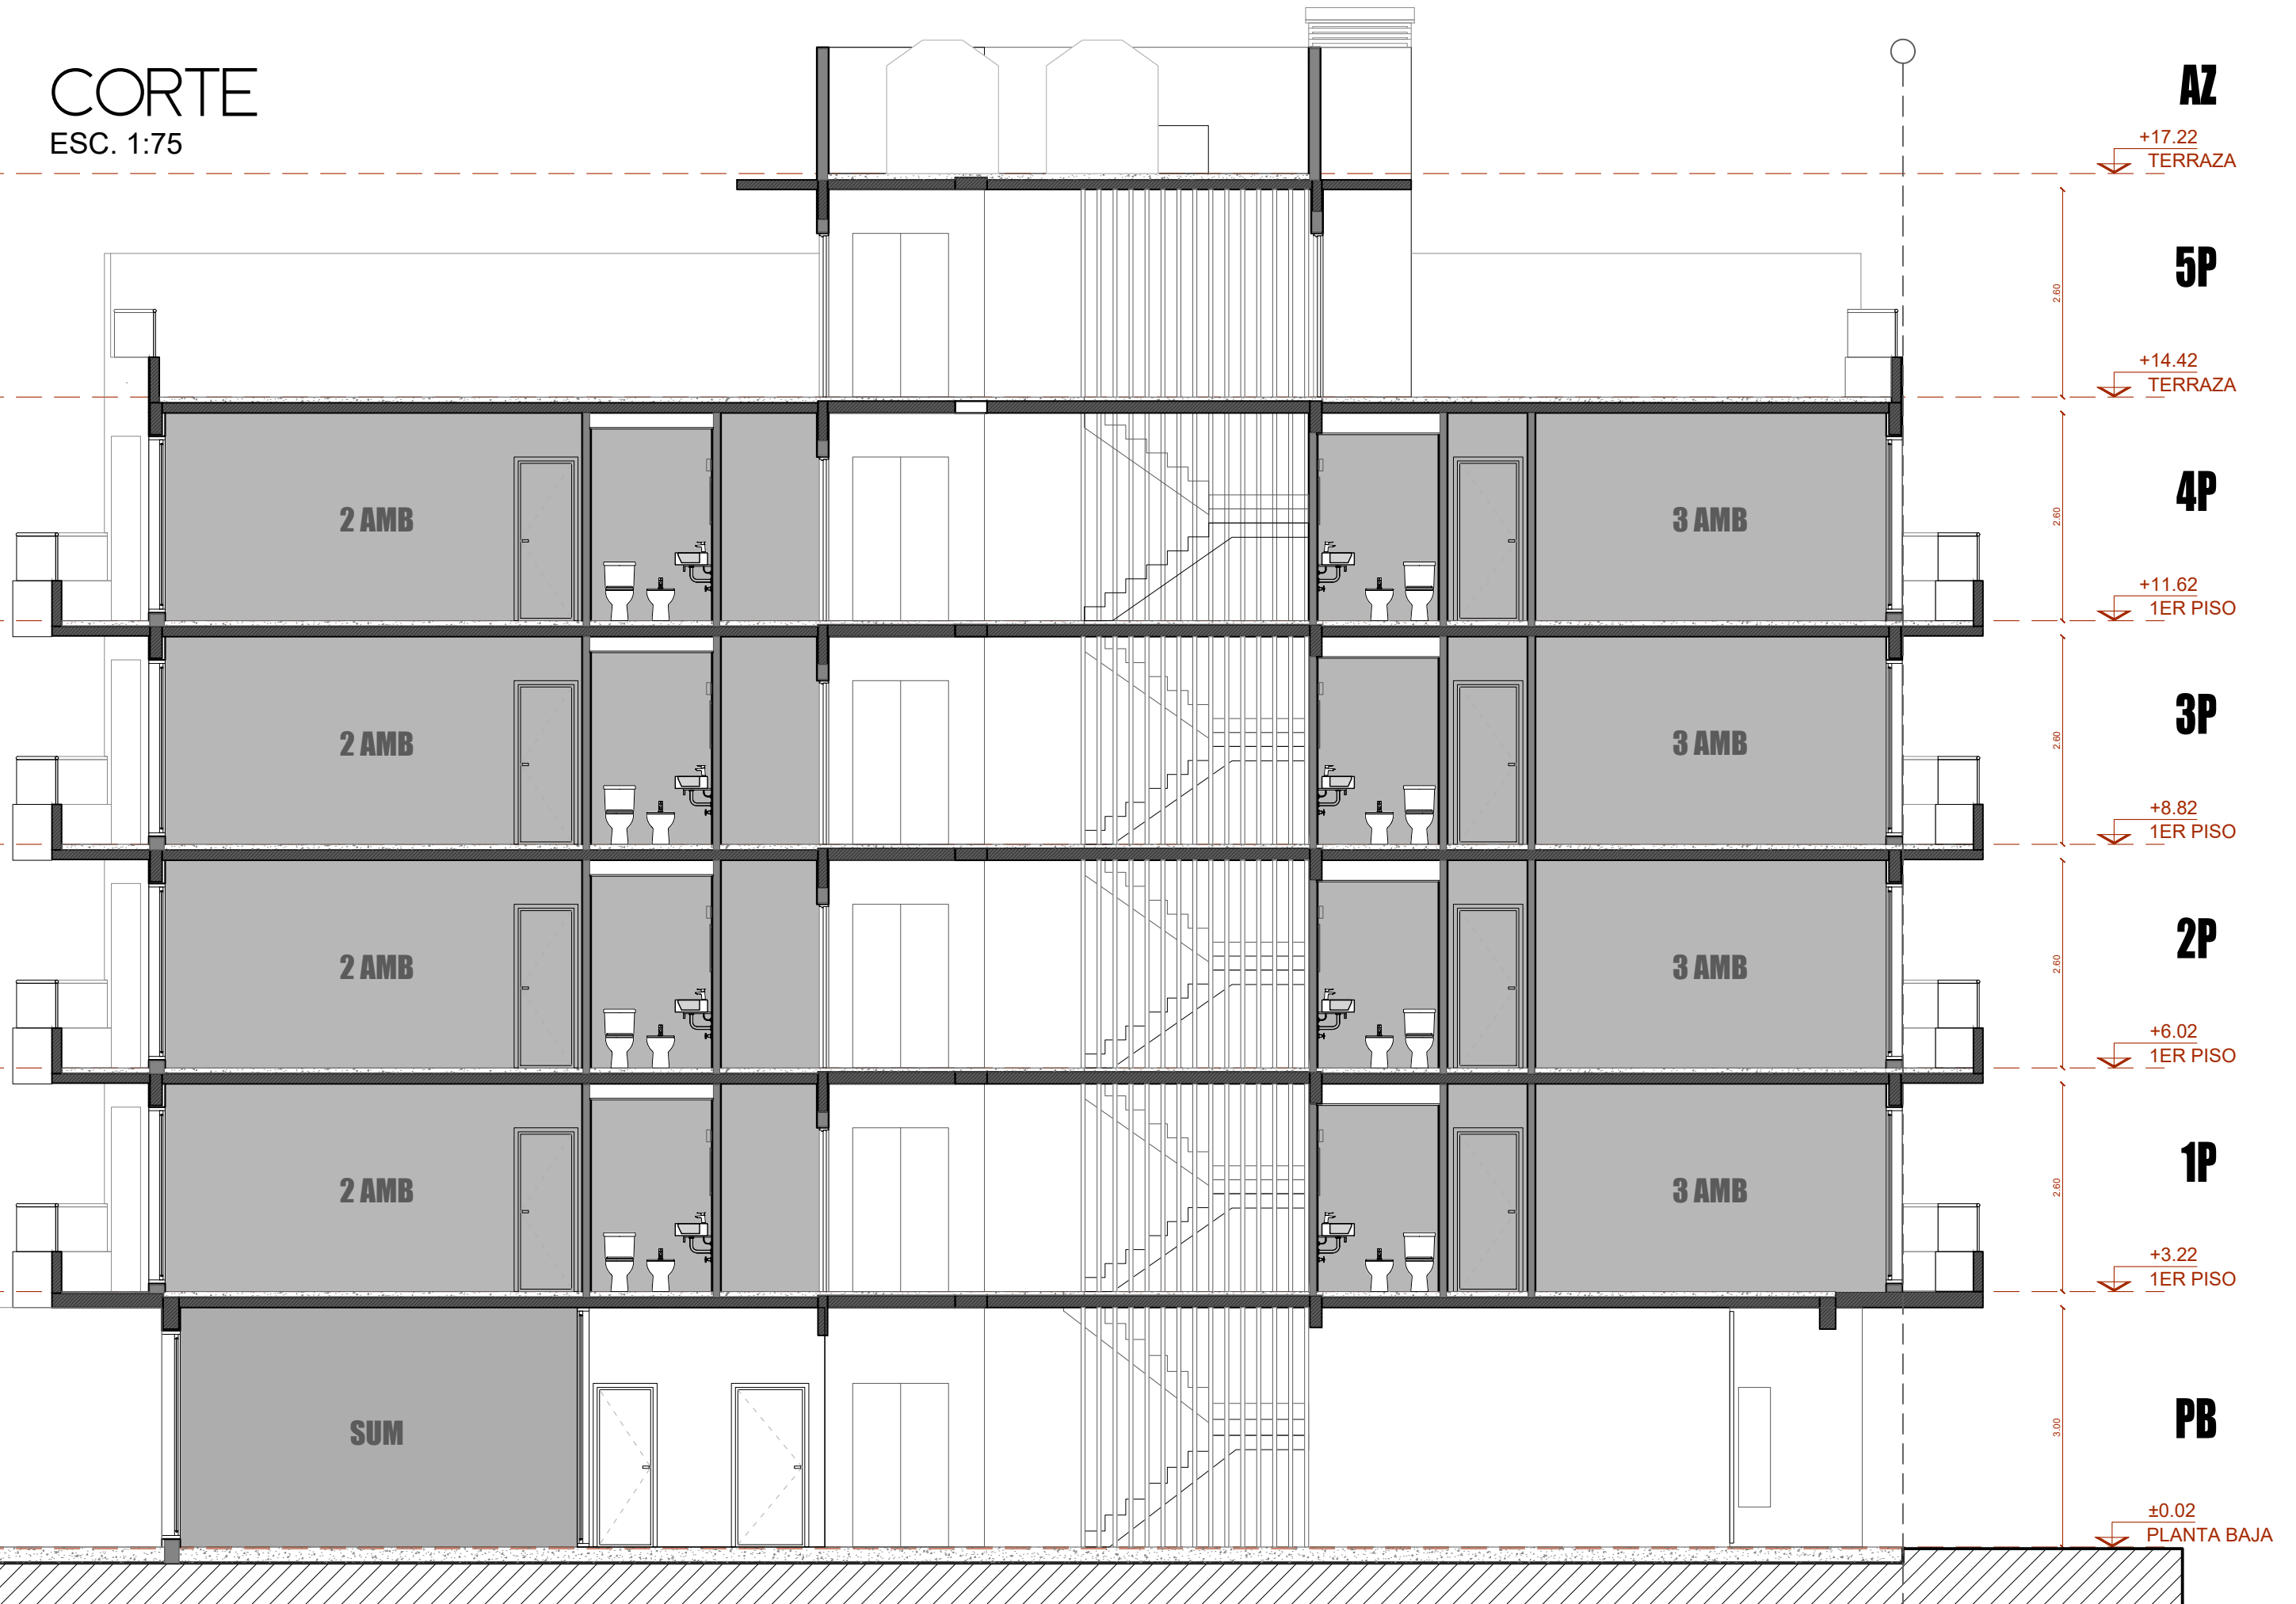


3 AMBIENTES ESC. 1:50

DEPARTAMENTO A

CUBIERTO: 72,53 m²
BALCÓN: 9,95 m²
TOTAL: 82,48 m²

TERRAZA		
4A	4B	4C
3A	3B	3C
2A	2B	2C
1A	1B	1C
PLANTA BAJA		

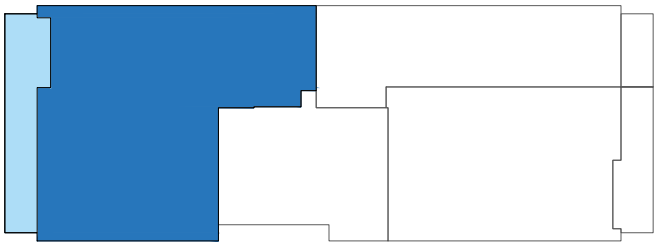

PLANTA TIPO





MONOAMBIENTE ESC. 1:50



DEPARTAMENTO B

CUBIERTO: 33,25 m²
BALCÓN: 4,15 m²
TOTAL: 37,40 m²

TERRAZA		
4A	4B	4C
3A	3B	3C
2A	2B	2C
1A	1B	1C
PLANTA BAJA		

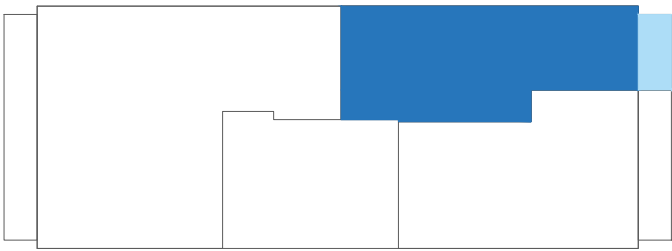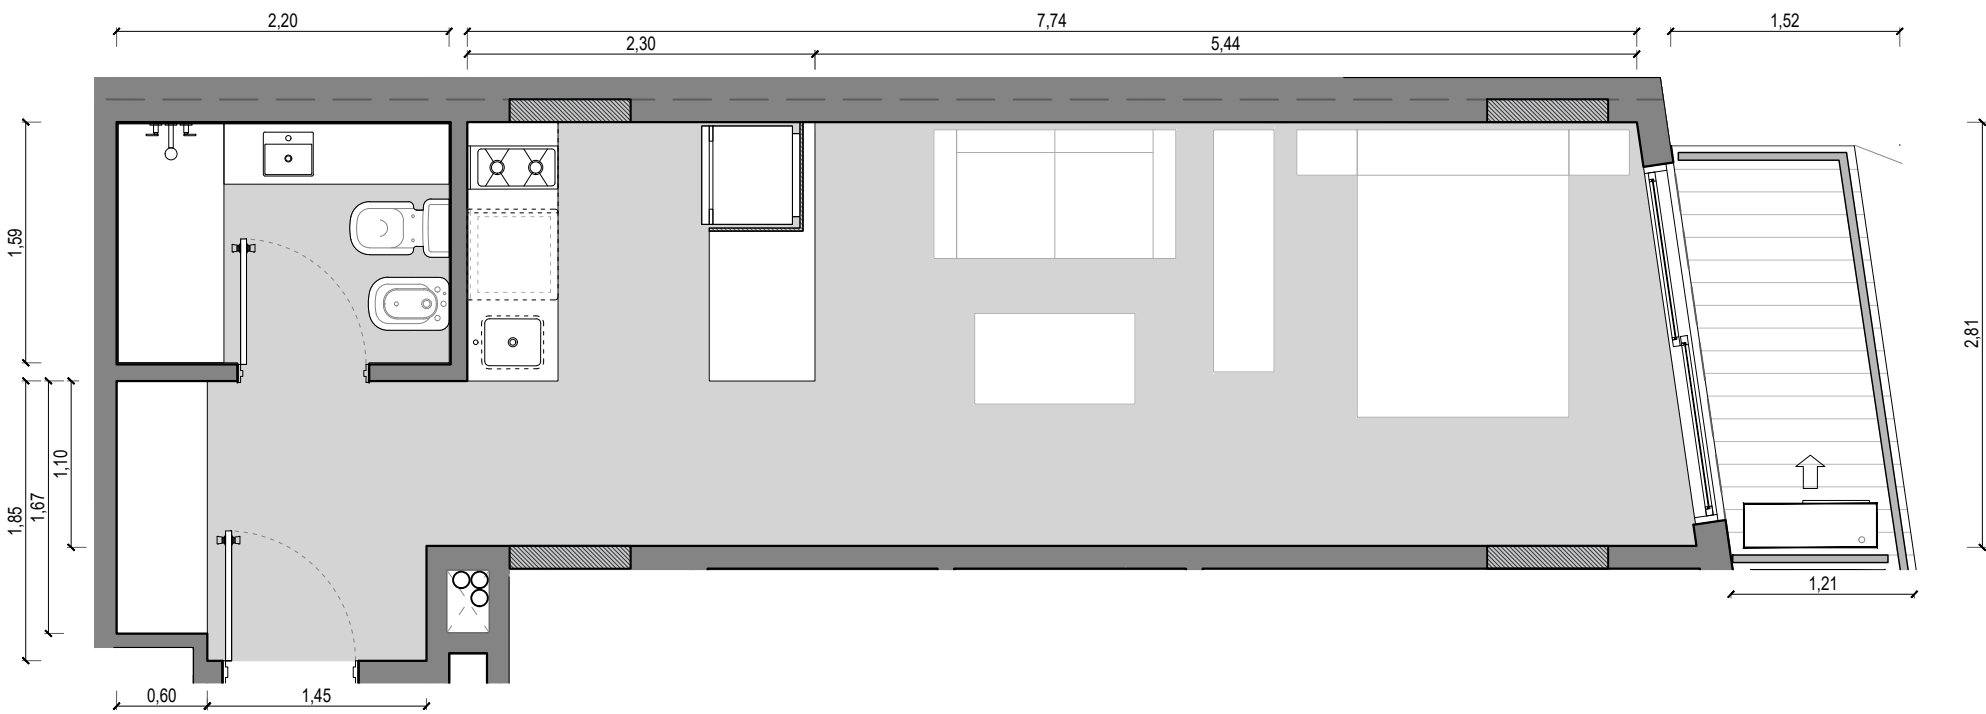



PLANTA TIPO

2 AMBIENTES ESC. 1:50

DEPARTAMENTO C
CUBIERTO: 46,54 m²
BALCÓN: 9,29 m²
TOTAL: 55,83 m²




TERRAZA		
4A	4B	4C
3A	3B	3C
2A	2B	2C
1A	1B	1C
PLANTA BAJA		

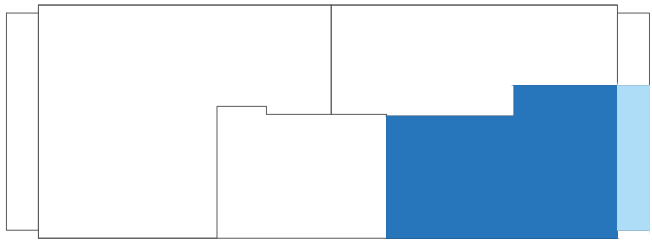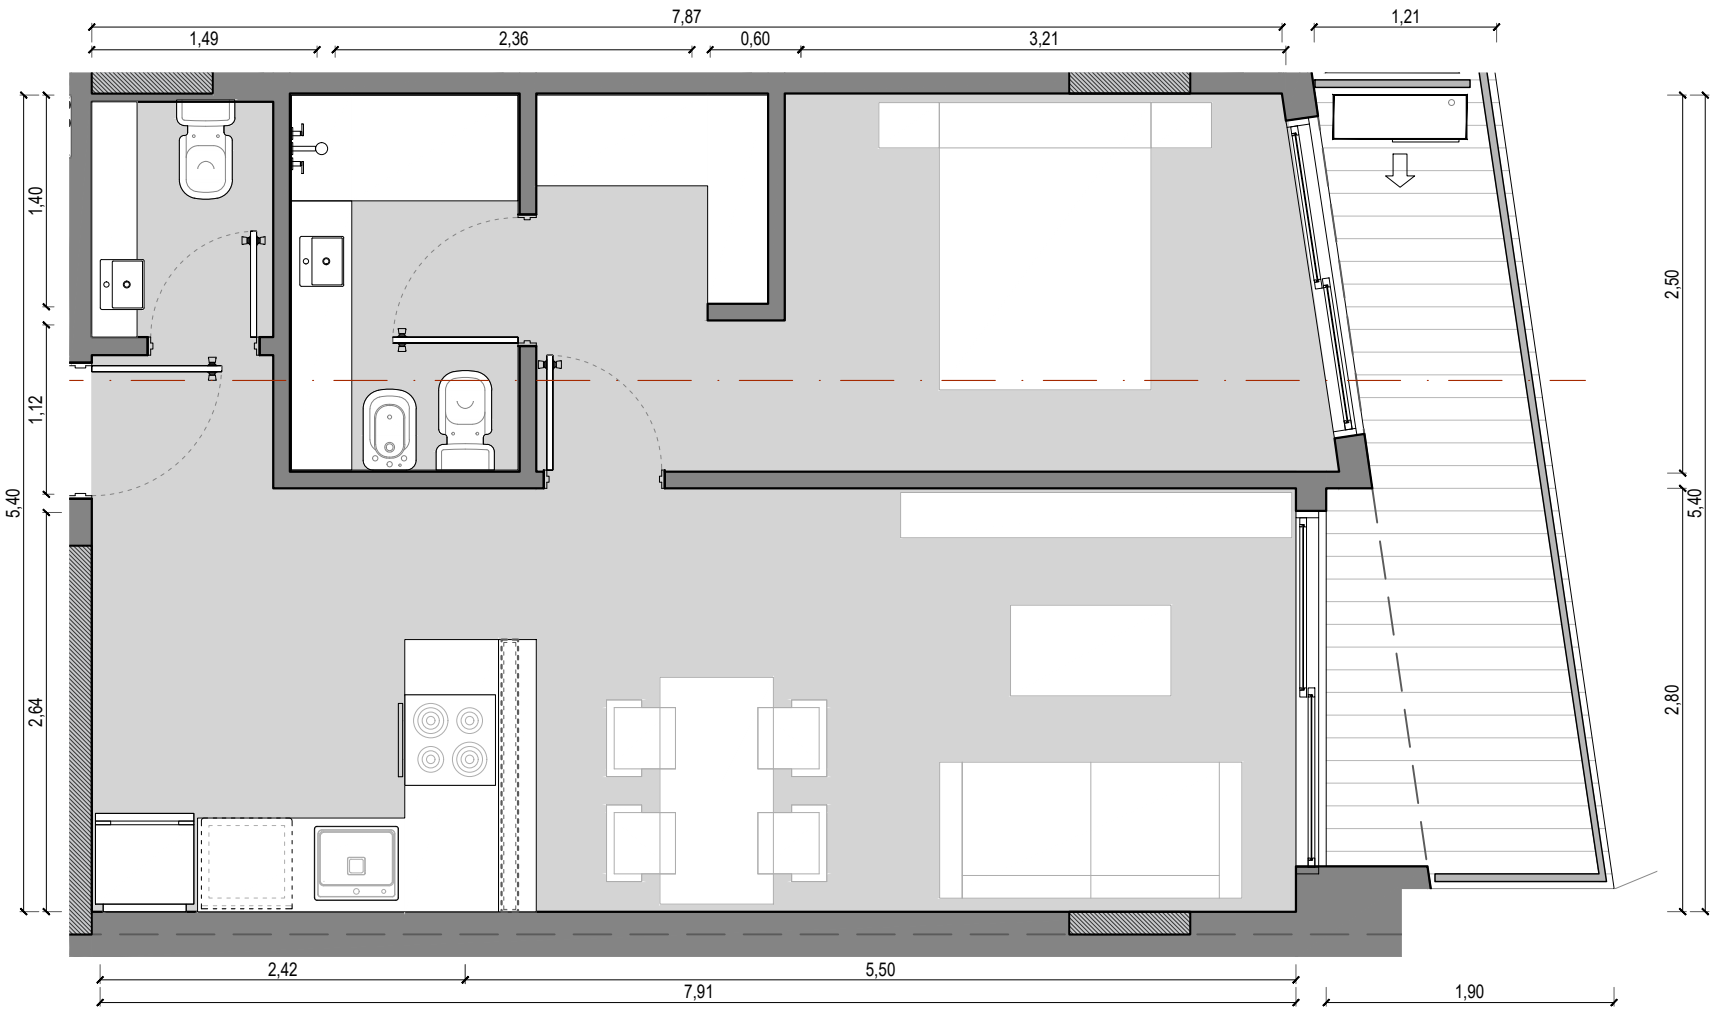


PLANTA TIPO


ESTRUCTURA S/PB
ESC. 1:75

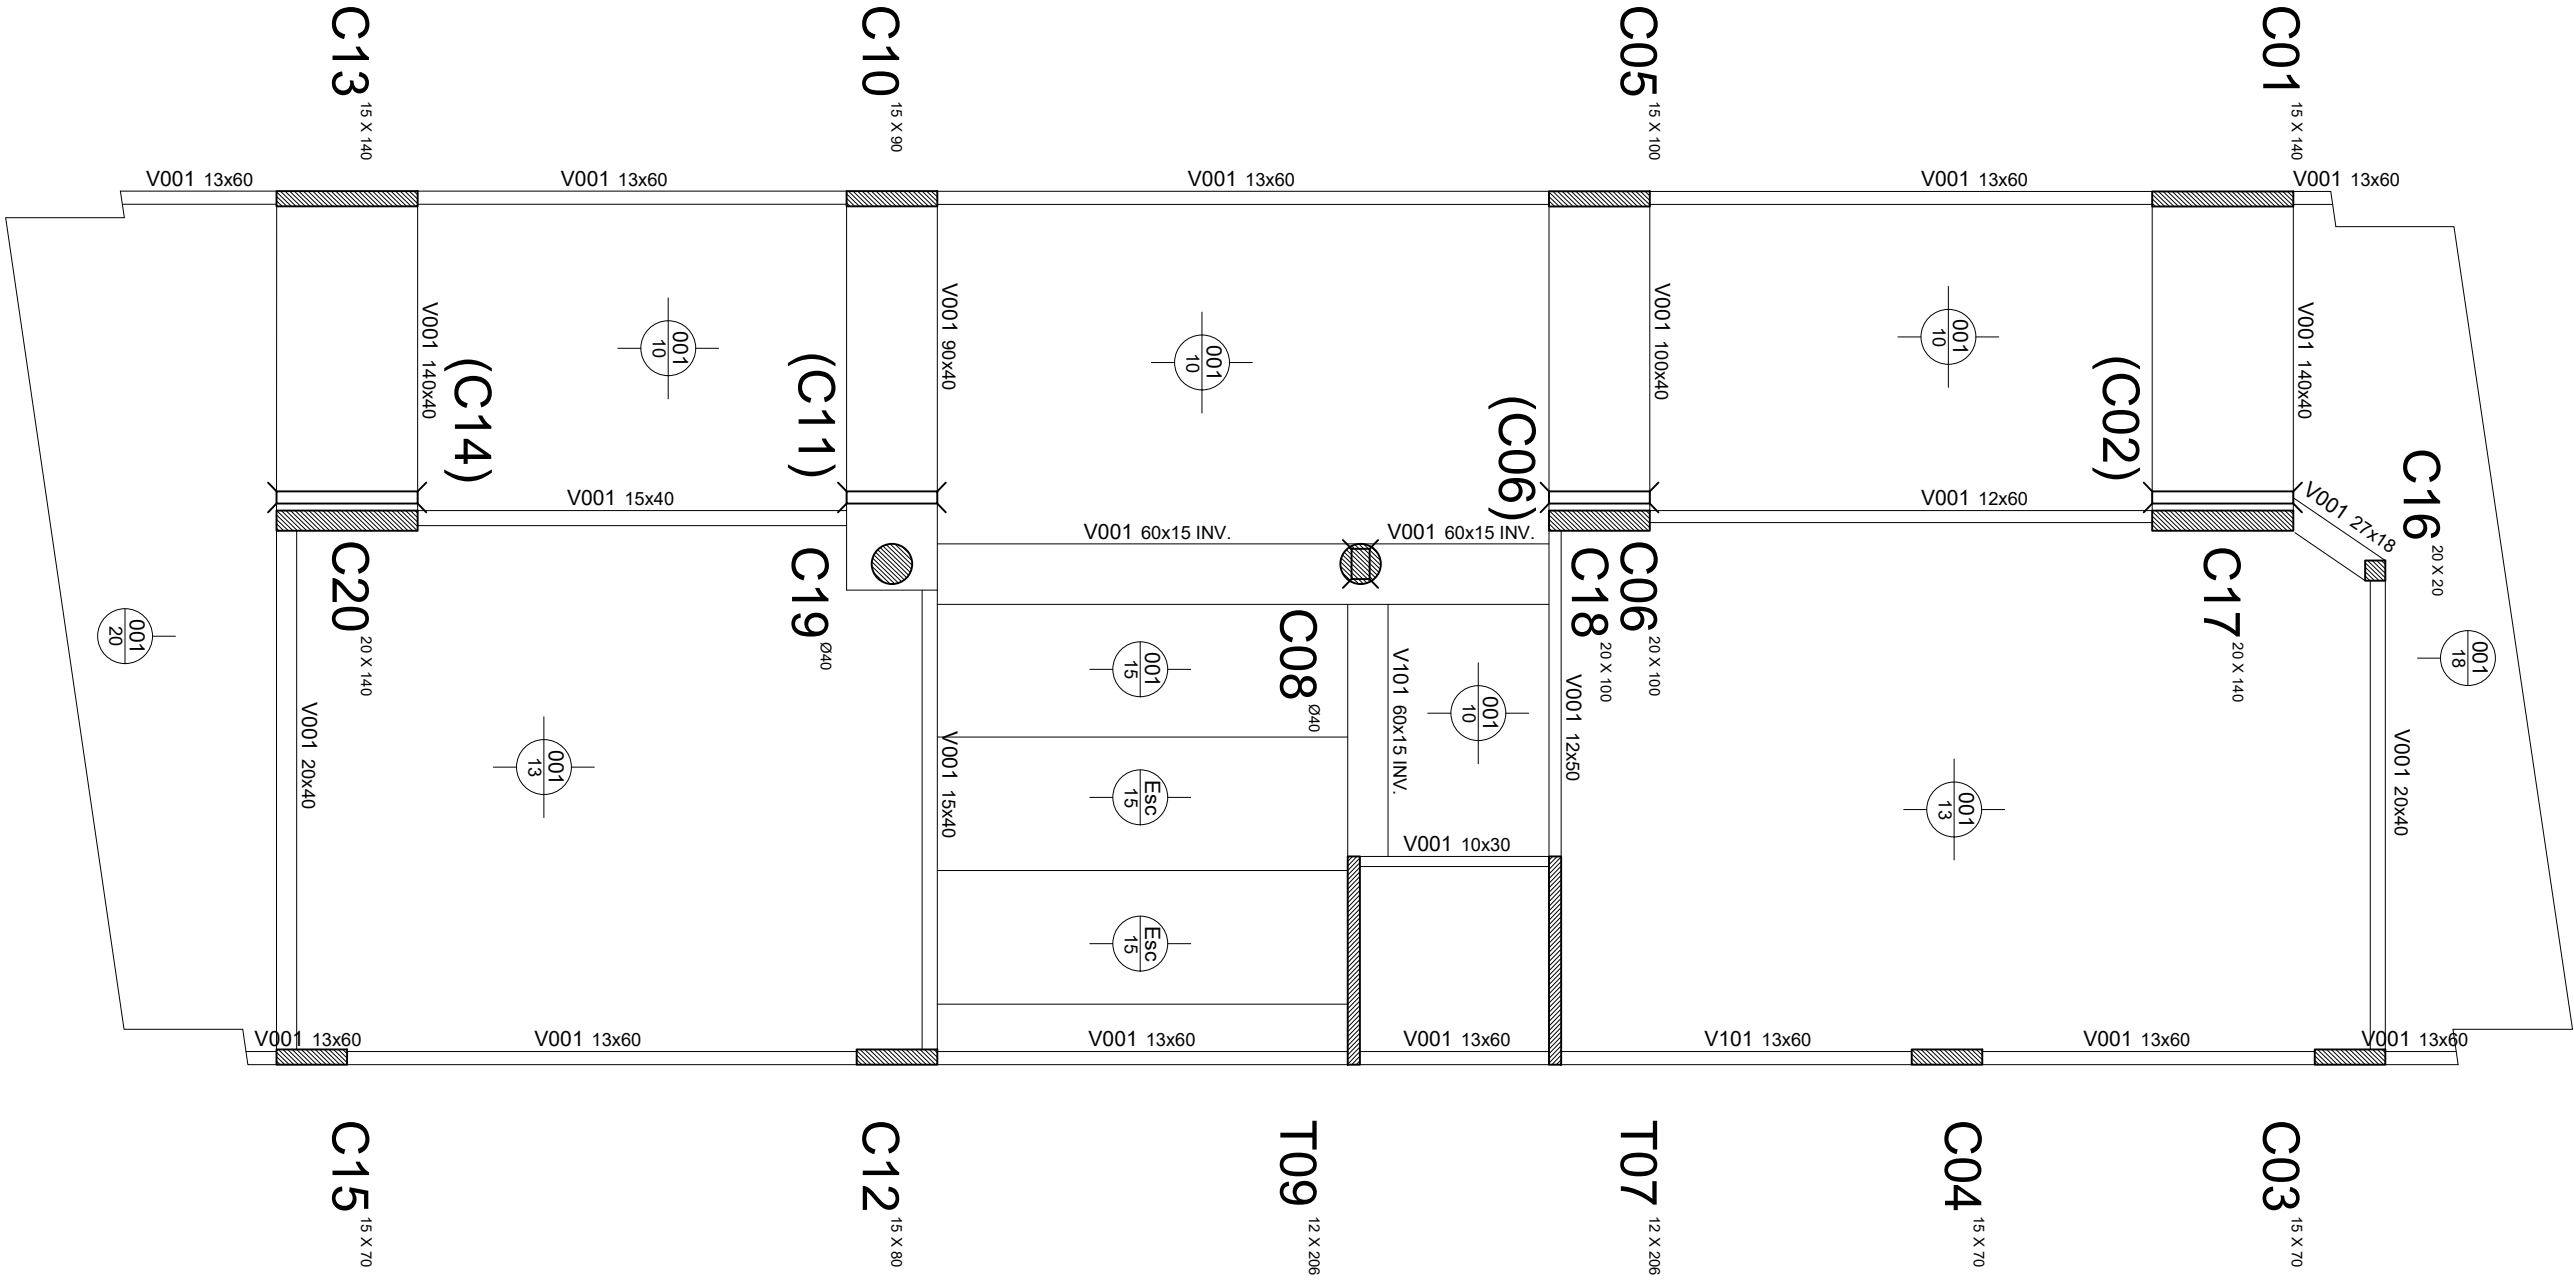

ESTRUCTURA S/I° A S/3°
ESC. 1:75

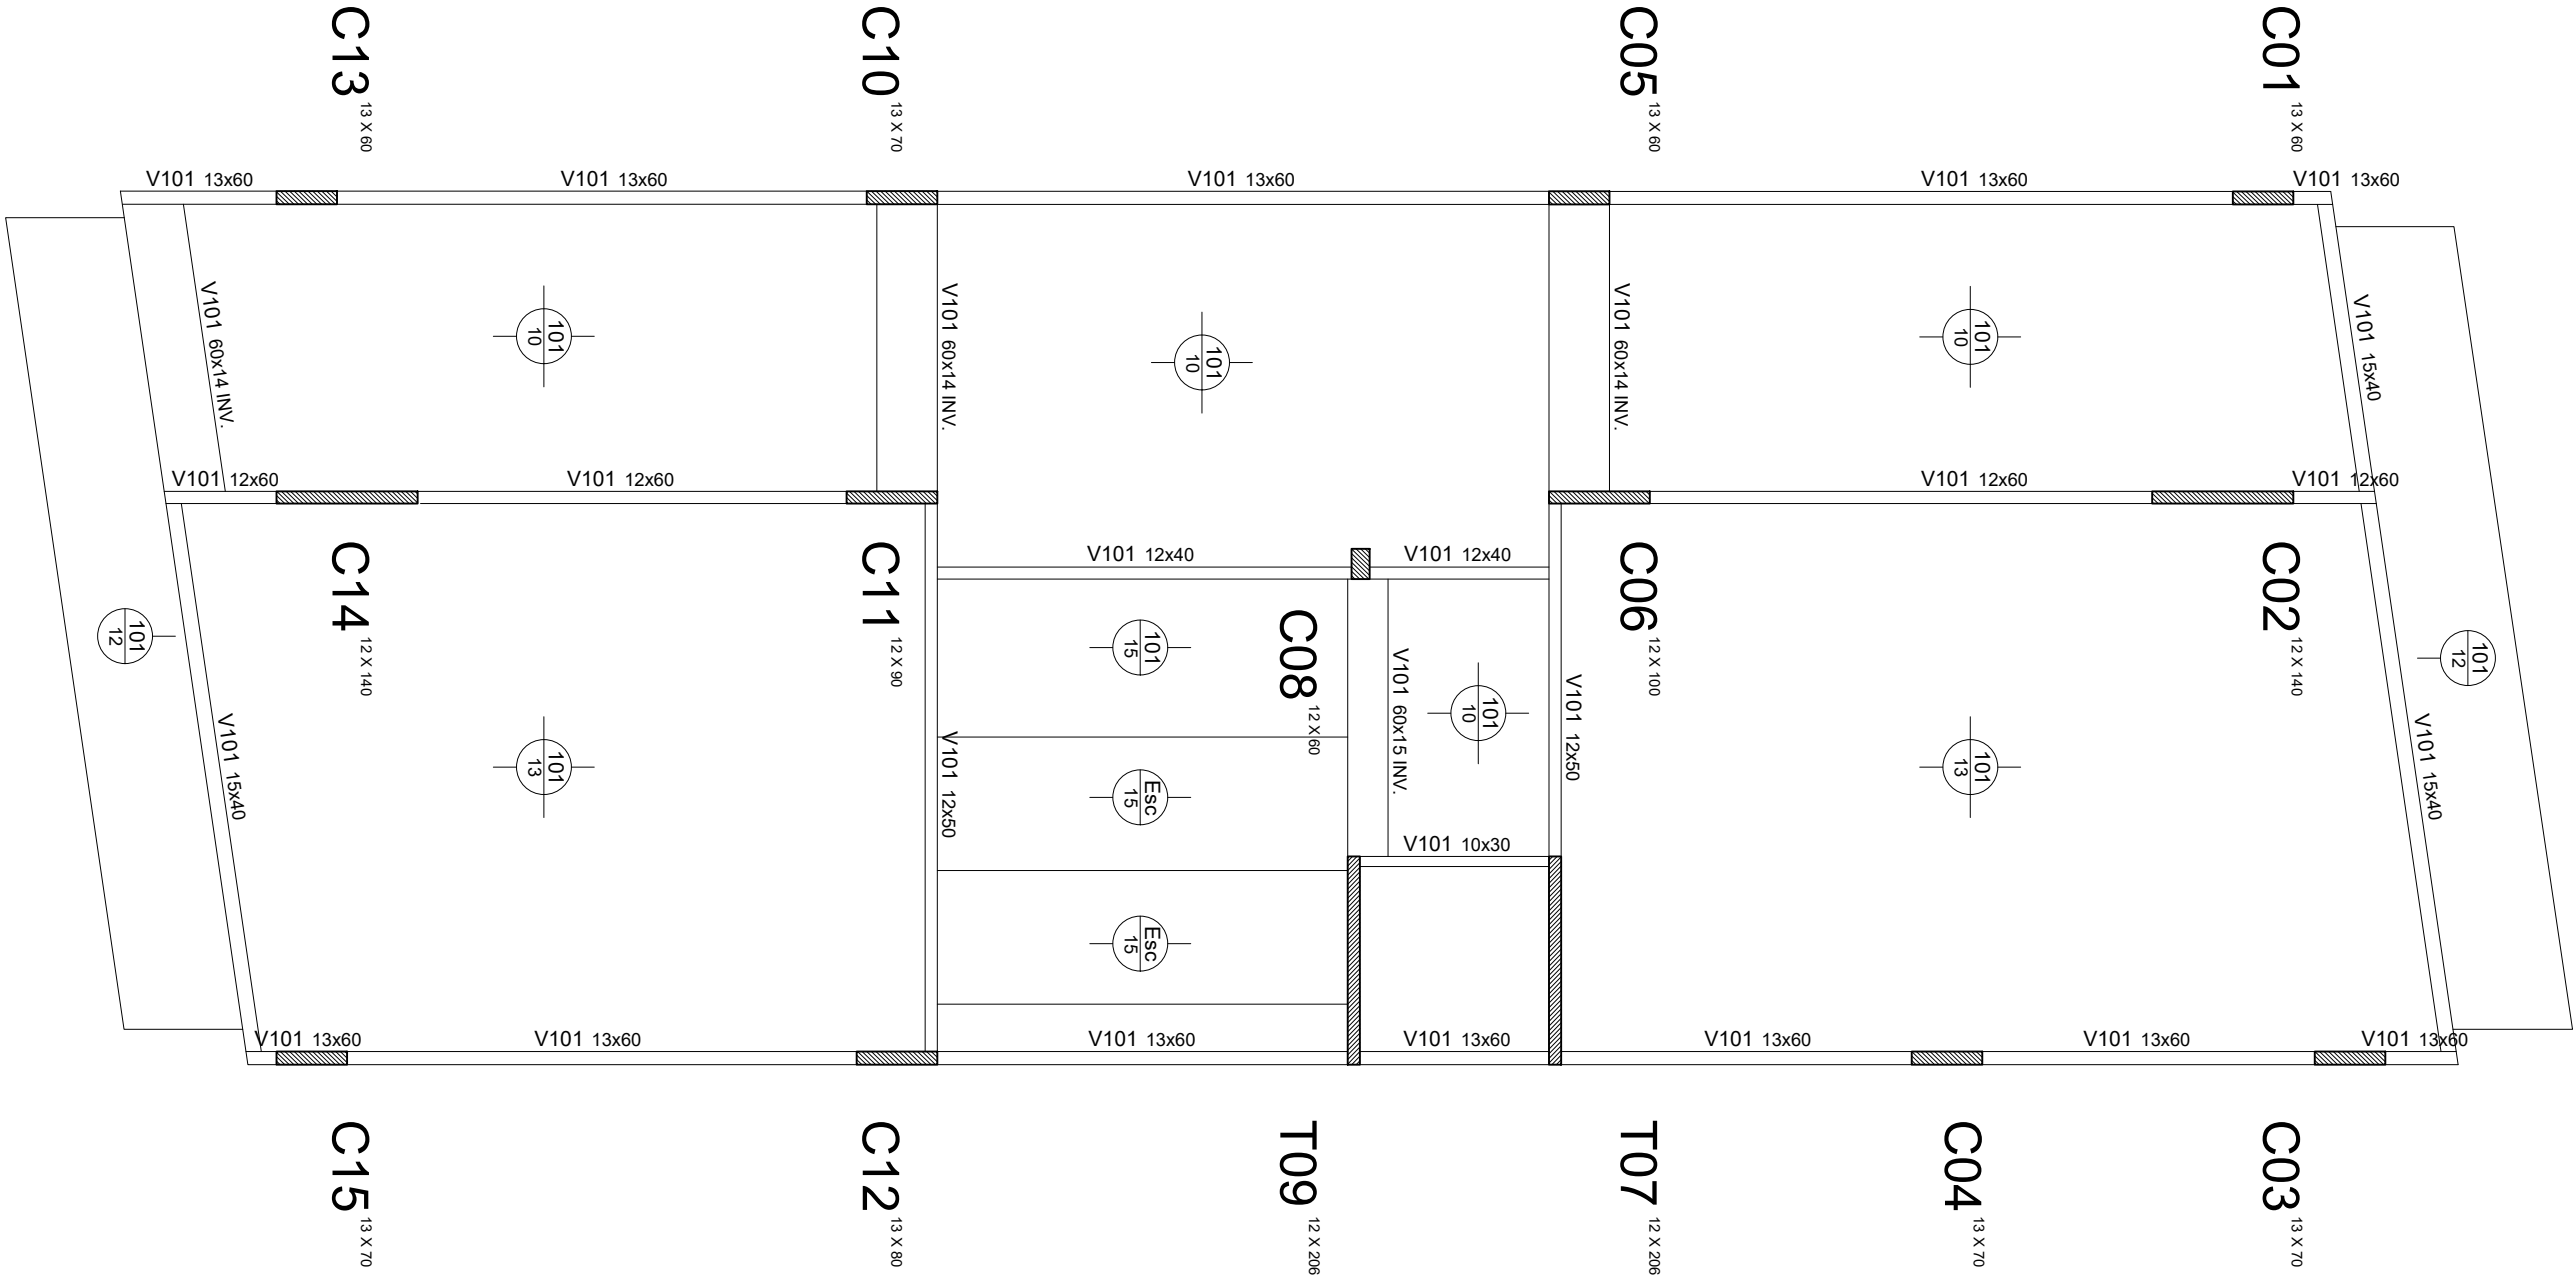

ESTRUCTURA S/4°
ESC. 1:75

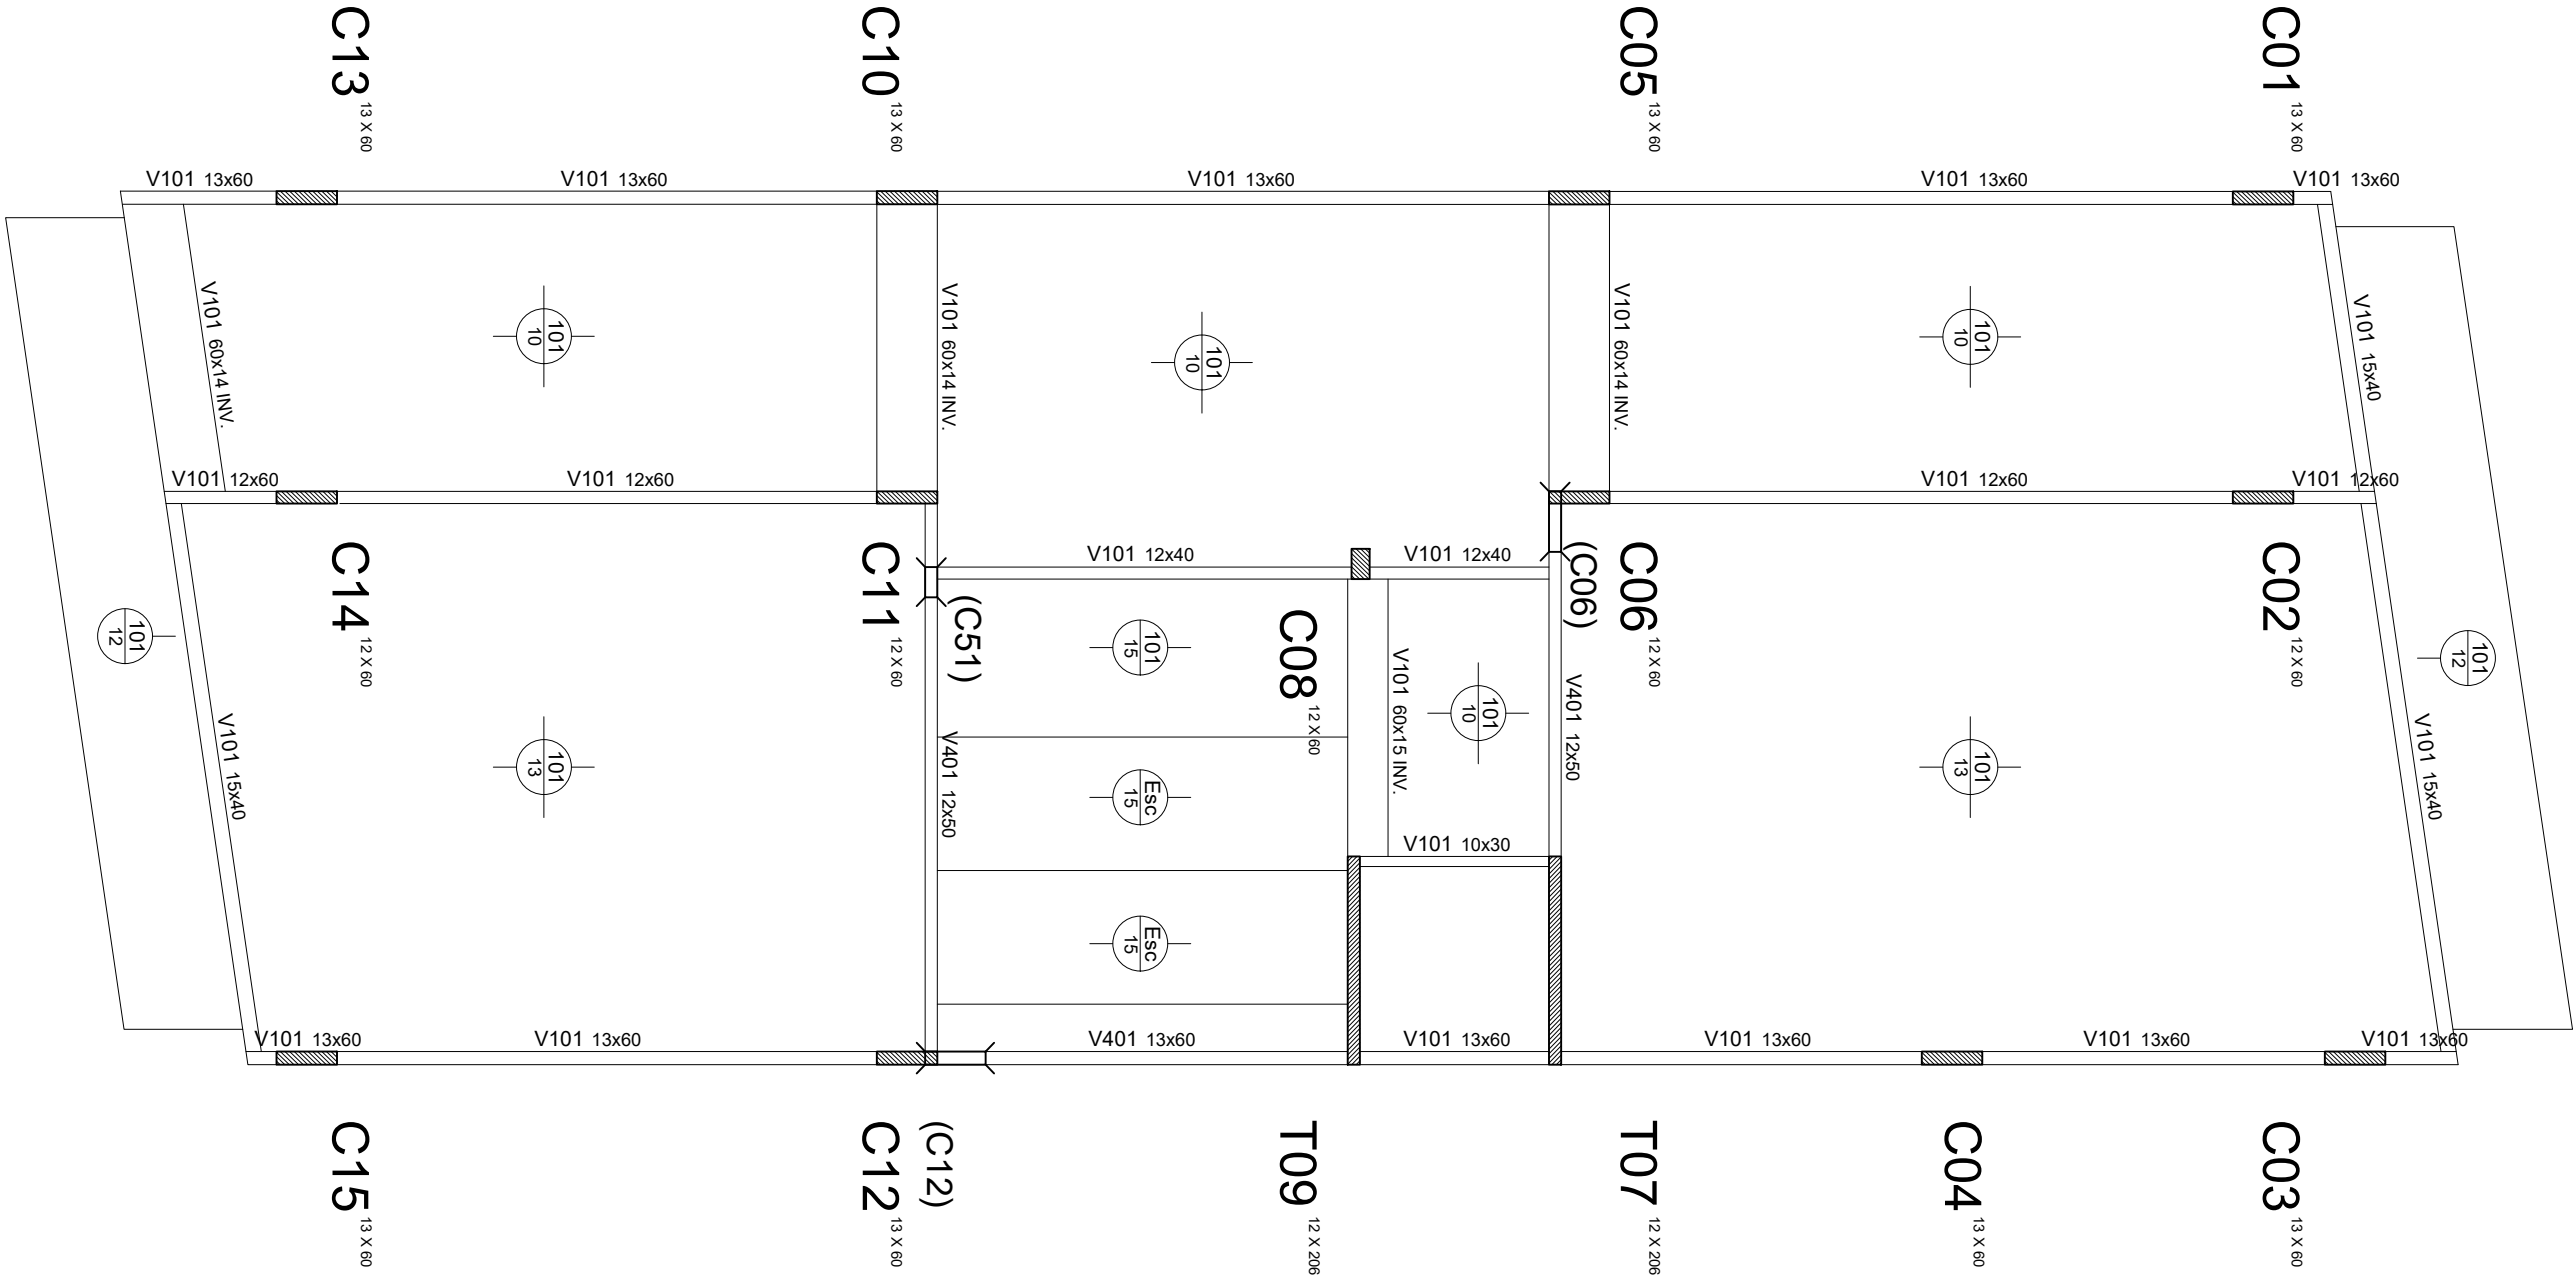

FACHADA

VERSIÓN ANTERIOR

- Ladrillo con baranda de hierro
- Balcones con cielorrasos de hormigón maquillado
- Hall de acceso con portón de hierro



FACHADA

PROPUESTA ACTUAL

- Ladrillo con baranda de hierro
- Balcones con cielorrasos de madera
- Hall de acceso con portón de varillado de madera



ACCESO

OPCIÓN 1 - HALL CON
CERRAMIENTO DE
MADERAS



ACCESO

OPCIÓN 2 - HALL CON
CERRAMIENTO DE
VIDRIO

