

SCHRAIFER
GOLDIN
ARQUITECTOS


VIDAL
AV. CABILDO
AV. GARCÍA DEL RÍO
PARQUE SAVEEDRA

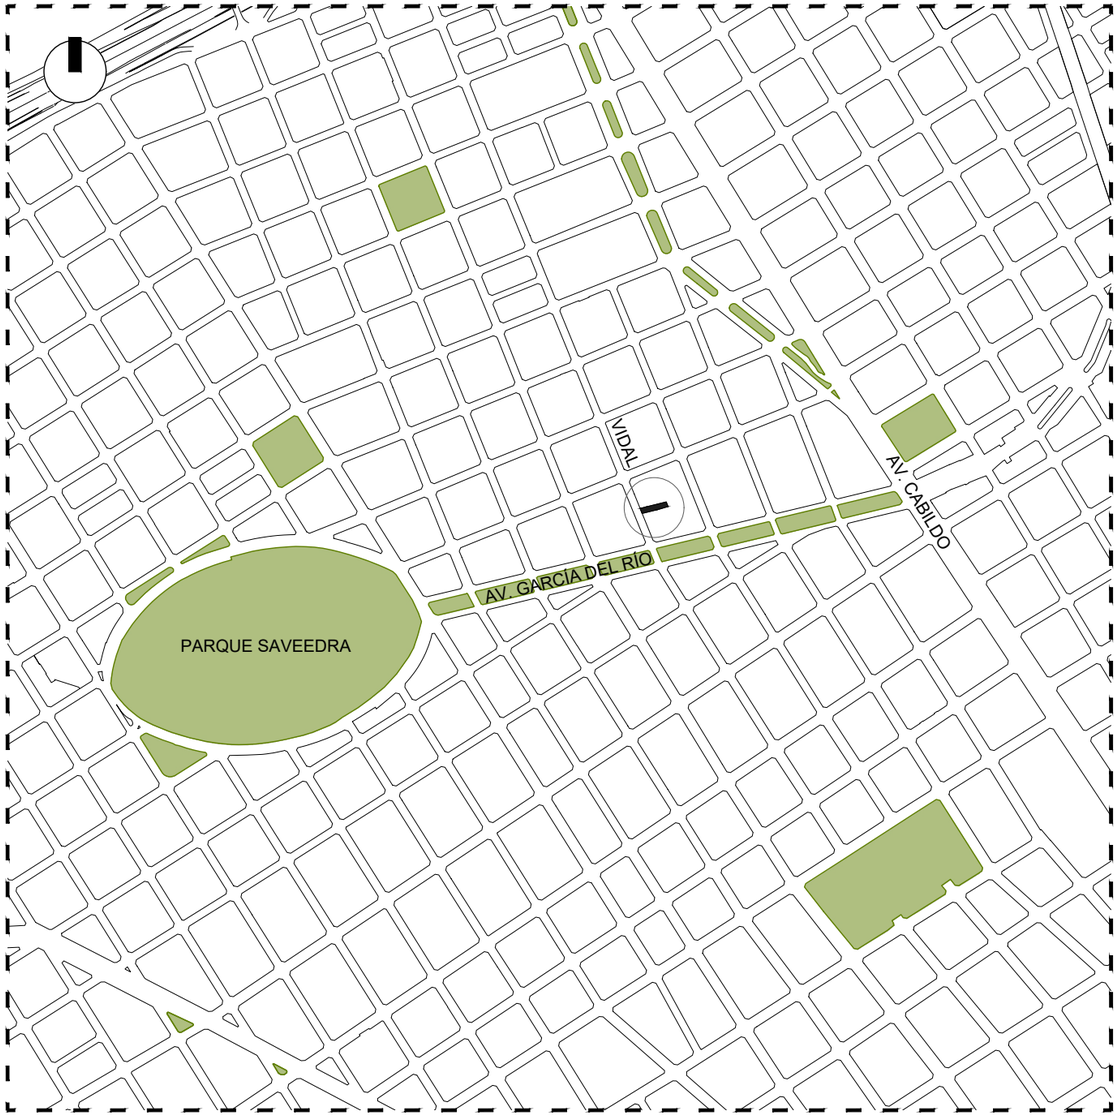


PLANTAS


ESC. 1:250

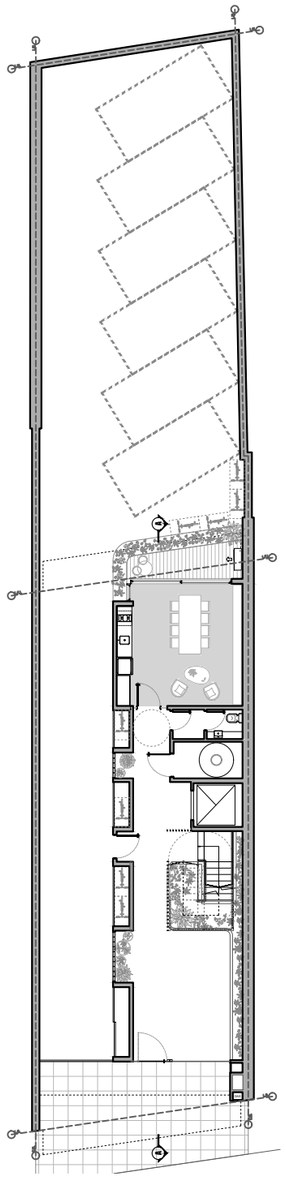

PLANTA BAJA

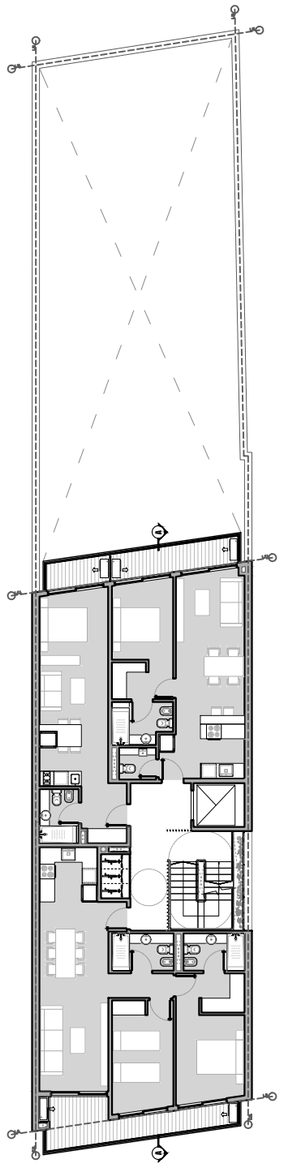


PLANTA TIPO
(1°-4°)

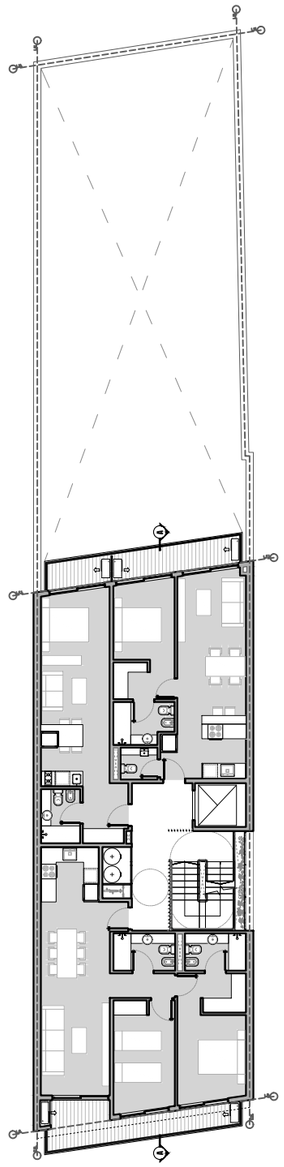

TERRAZA

PLANTA BAJA

ESC. 1:75

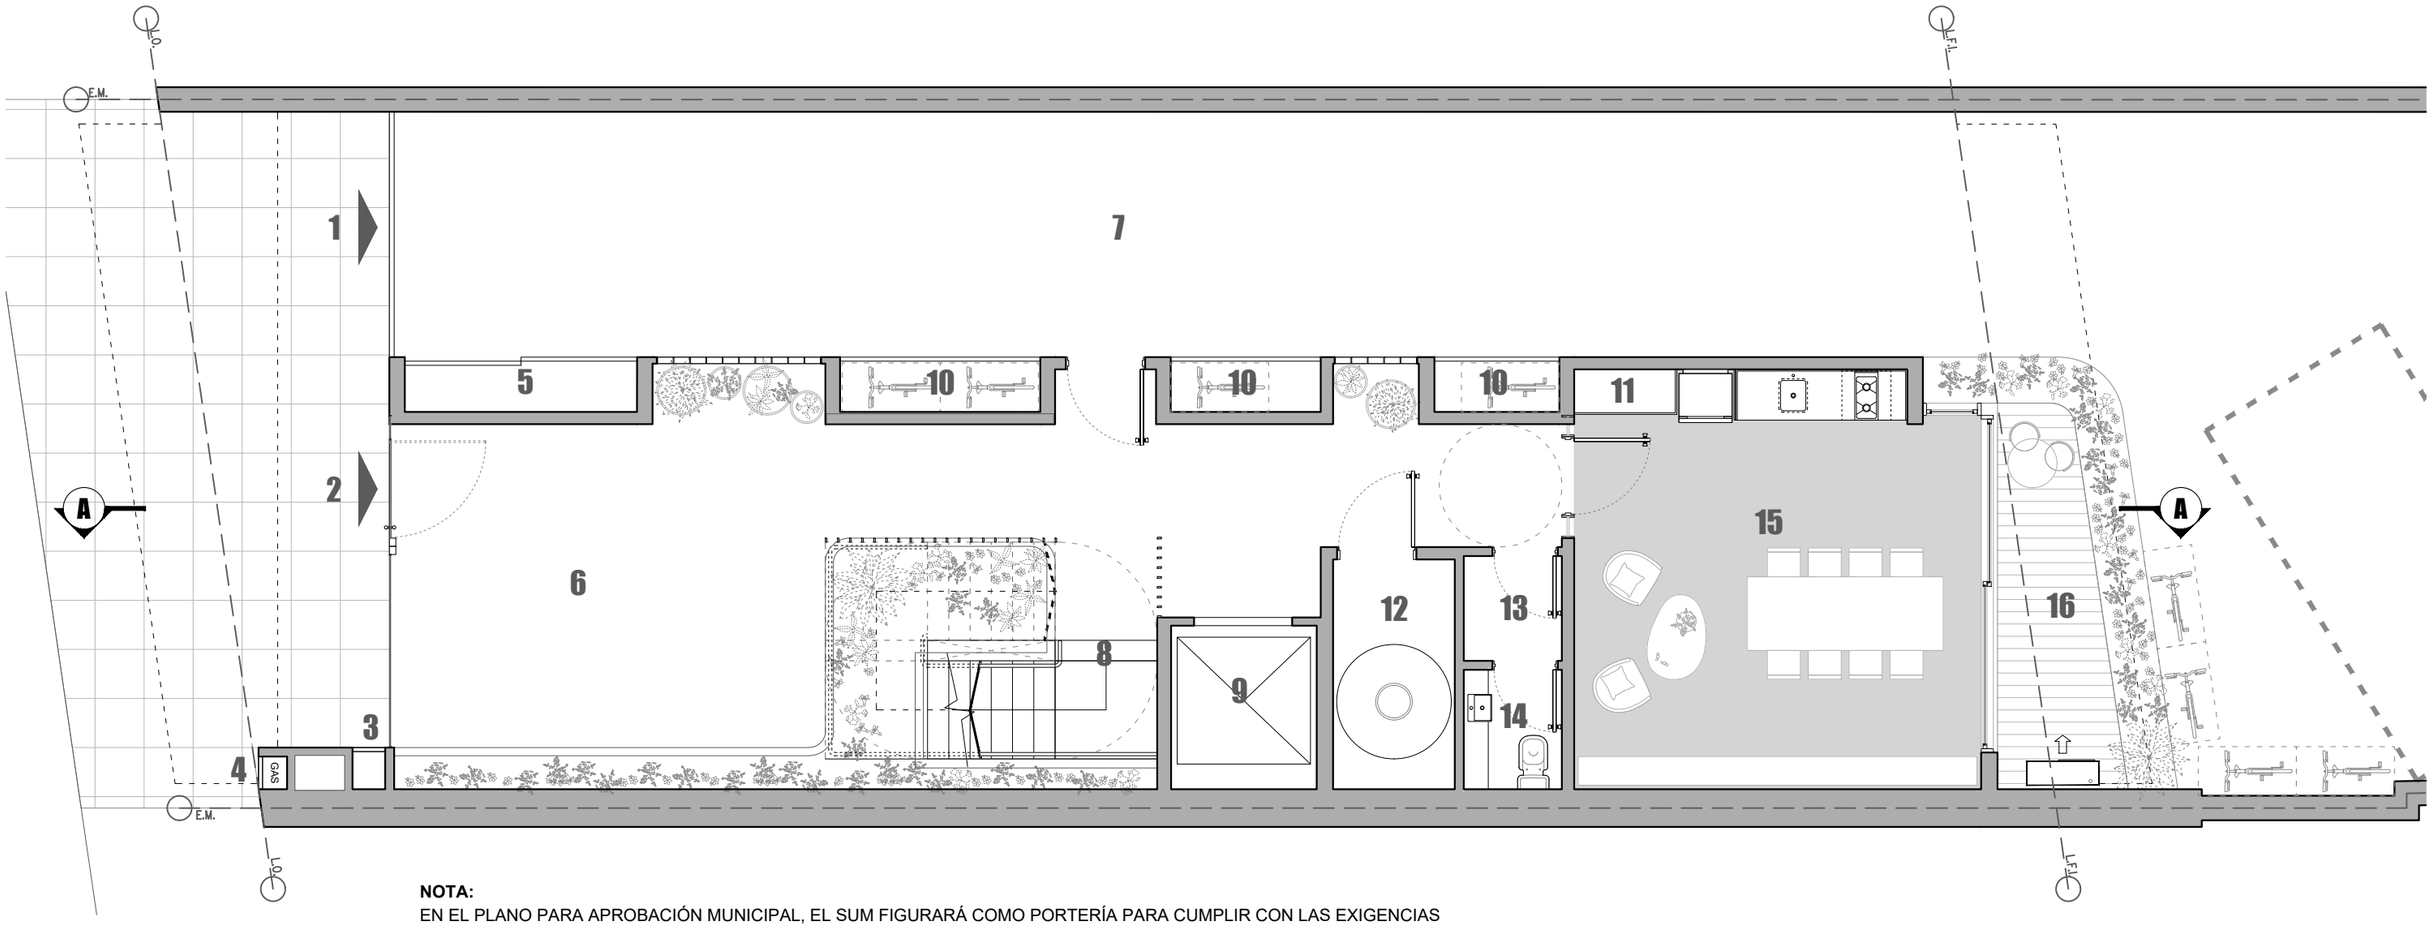

NOTA:
EN EL PLANO PARA APROBACIÓN MUNICIPAL, EL SUM FIGURARÁ COMO PORTERÍA PARA CUMPLIR CON LAS EXIGENCIAS DE M2 MÍNIMOS PARA PERSONAL DE MANTENIMIENTO SEGÚN CÓDIGO.

REFERENCIAS

1. ACCESO VEHÍCULAR
2. ACCESO PEATONAL
3. BUZON EDESUR
4. NICHO DE GAS
5. MEDIDORES
6. HALL ACCESO
7. CIRCULACIÓN VEHÍCULAR
8. ESCALERA
9. ASCENSOR
10. BAULERA / BICICLETERO
11. GUARDADO
12. SALA DE BOMBEO
13. AUXILIAR PORTERÍA
14. BAÑO
15. SUM
16. EXPANSIÓN SUM


SUPERFICIES

- COCHERAS
- CUBIERTAS: 69.17 m^2
- SEMICUBIERTAS: 4.32 m^2
- DESCUBIERTAS: 157.62 m^2 (6 ESPACIOS)

- HALL DE ACCESO: 76.47 m^2
- BAULERAS: 4.63 m^2

PLANTA TIPO (1°-3°)

ESC. 1:75

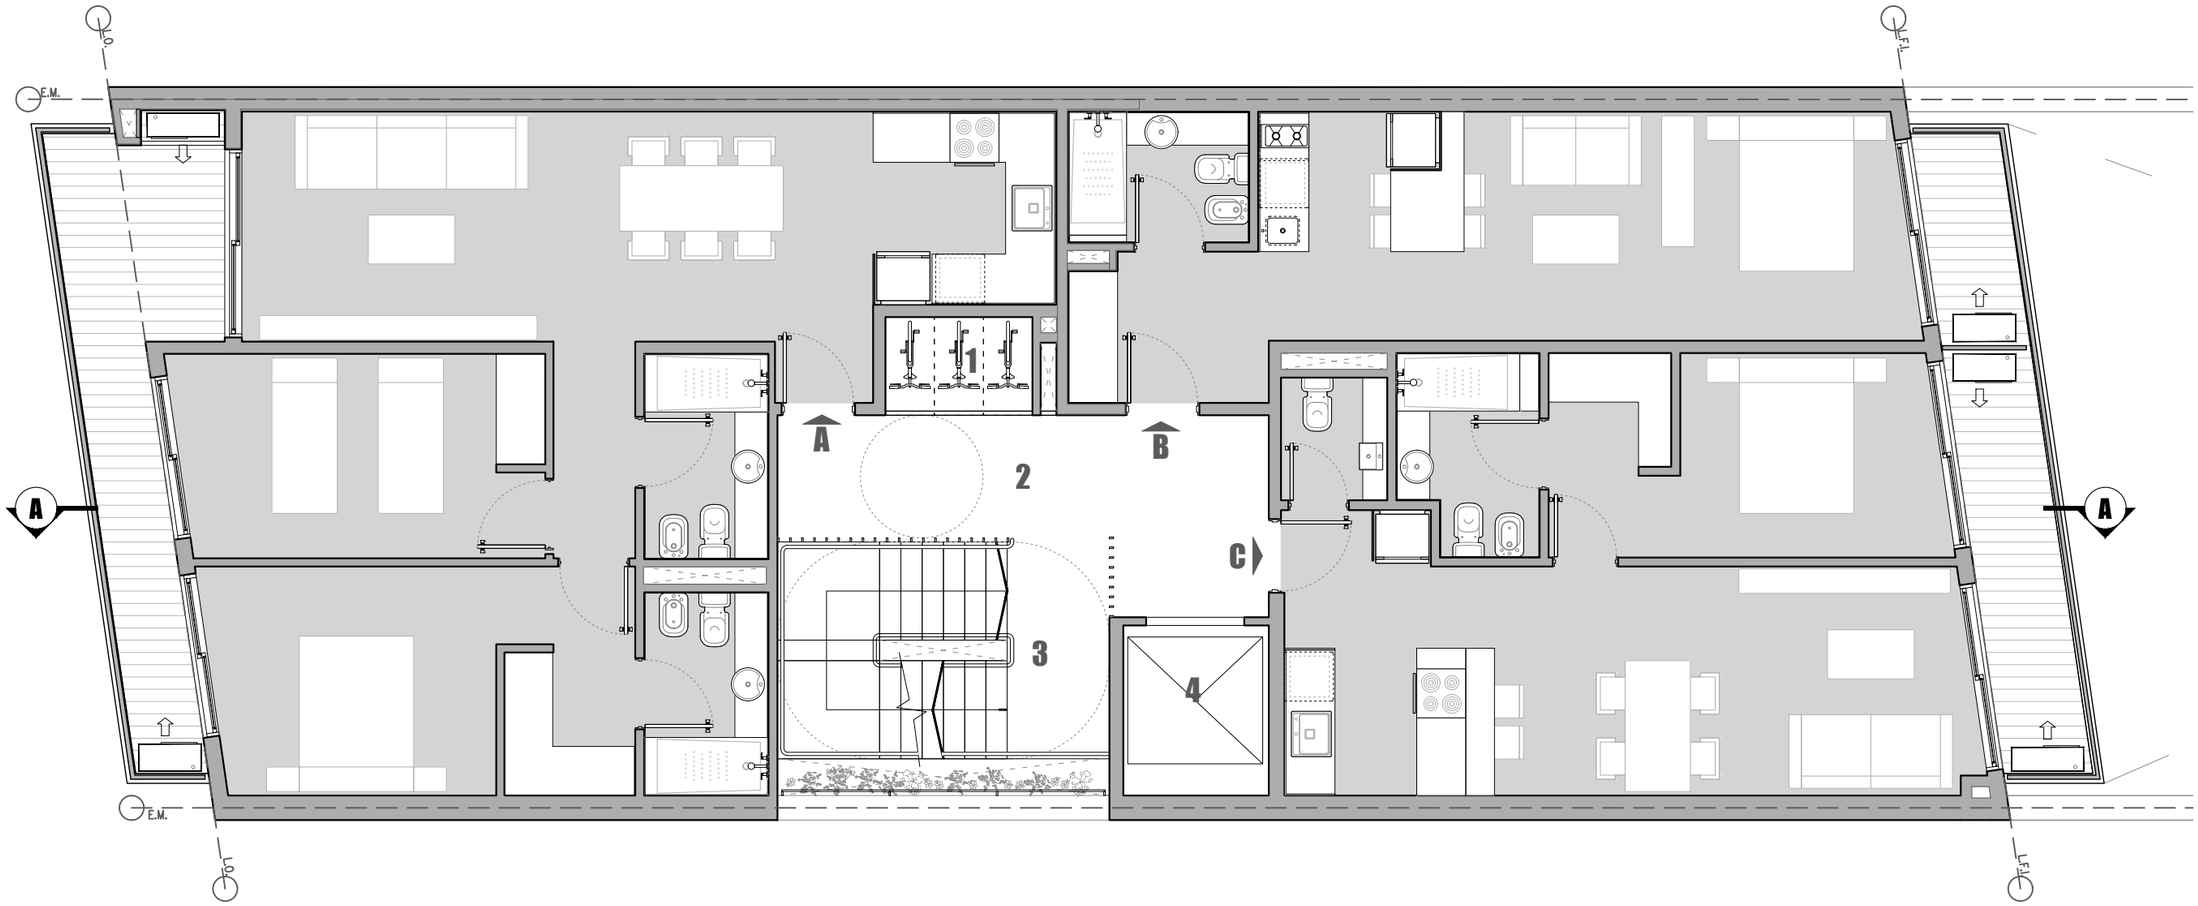

REFERENCIAS


1. BAULERAS / BICICLETEROS
2. PALIER
3. ESCALERA
4. ASCENSOR

SUPERFICIES

- UNIDAD A: 71.36m² cub. / 11.07m² semi.
- UNIDAD B: 33,61m² cub. / 3.32m² semi.
- UNIDAD C: 47.81m² cub. / 6.46m² semi.
- CIRCULACIONES: 31.51m²
- BAULERAS: 2.86m²

PLANTA TIPO (4°)

ESC. 1:75

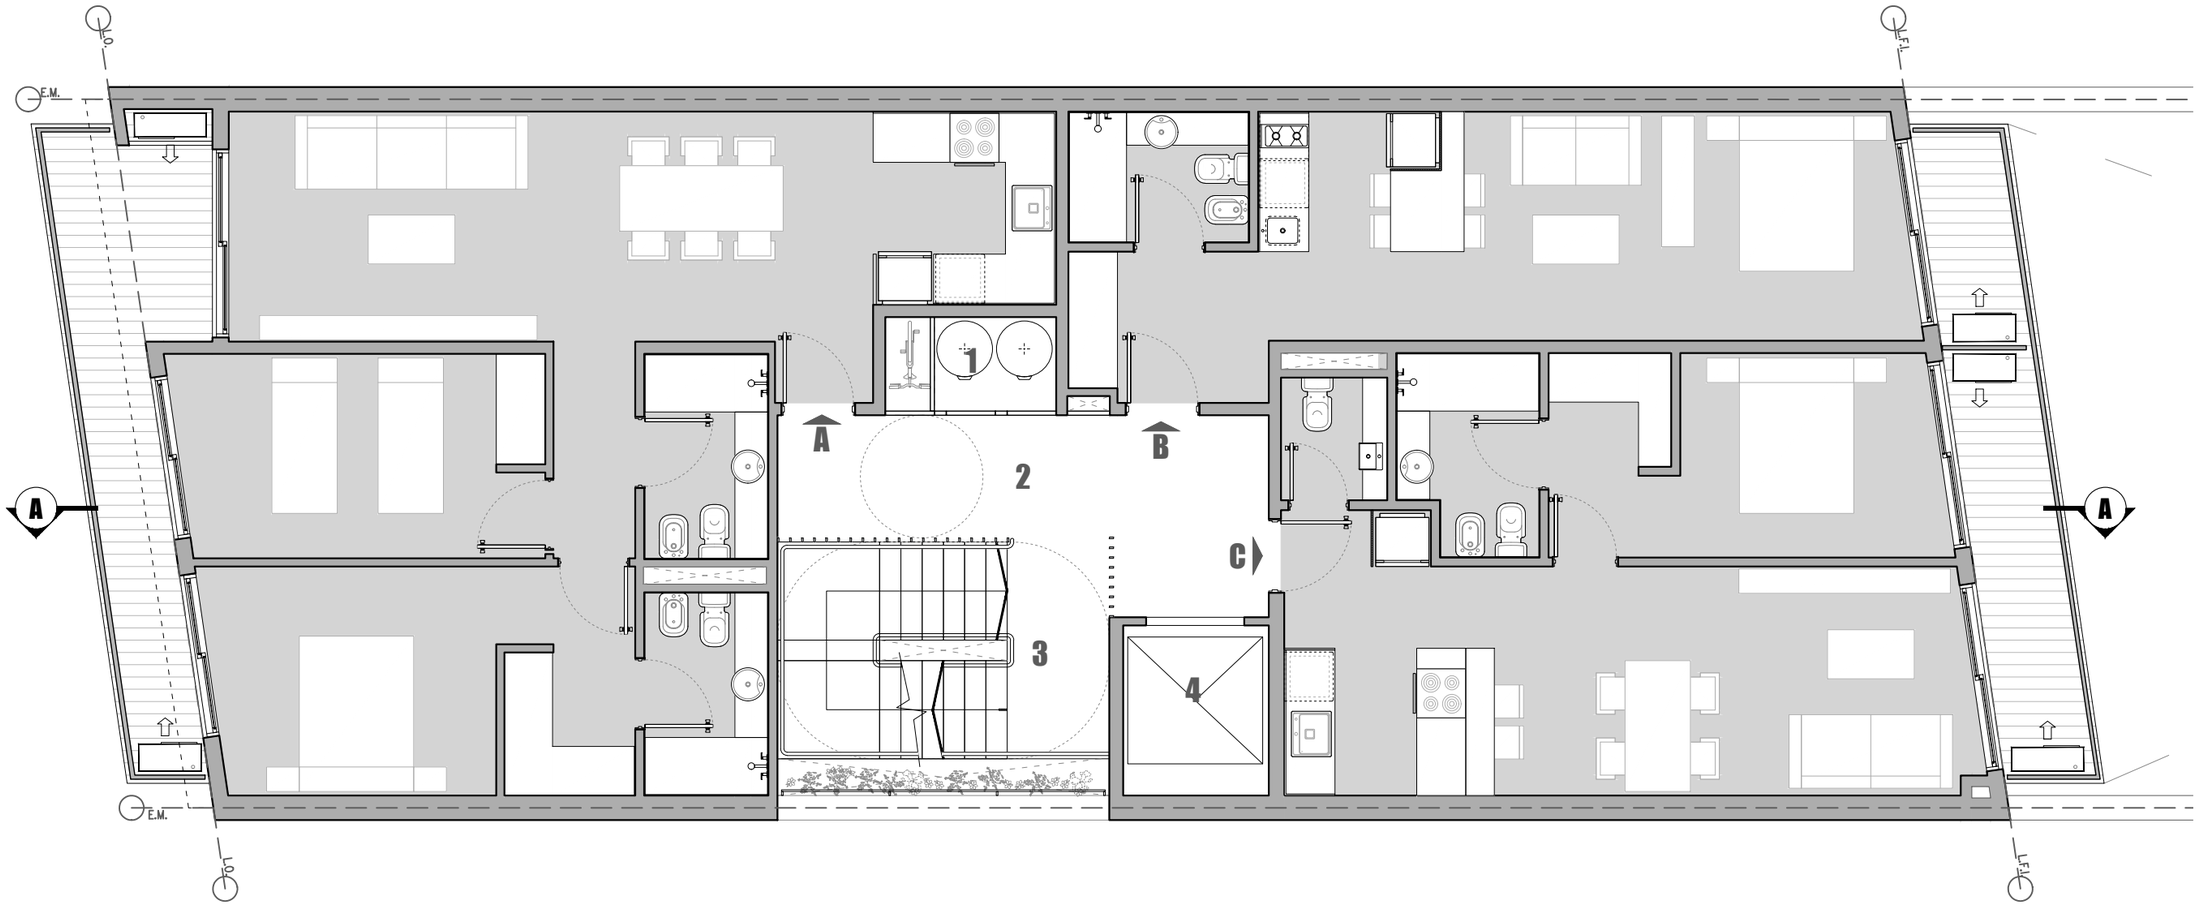

REFERENCIAS


1. BAULERA / TERMOTANQUES
2. PALIER
3. ESCALERA
4. ASCENSOR

SUPERFICIES

- UNIDAD A: 72,72m² cub. / 9.95m² semi.
- UNIDAD B: 33,25m² cub. / 3,32m² semi.
- UNIDAD C: 46,56m² cub. / 7,68m² semi.
- CIRCULACIONES: 31,92m²
- BAULERA: 0.86m²

PLANTA TERRAZAS

ESC. 1:75

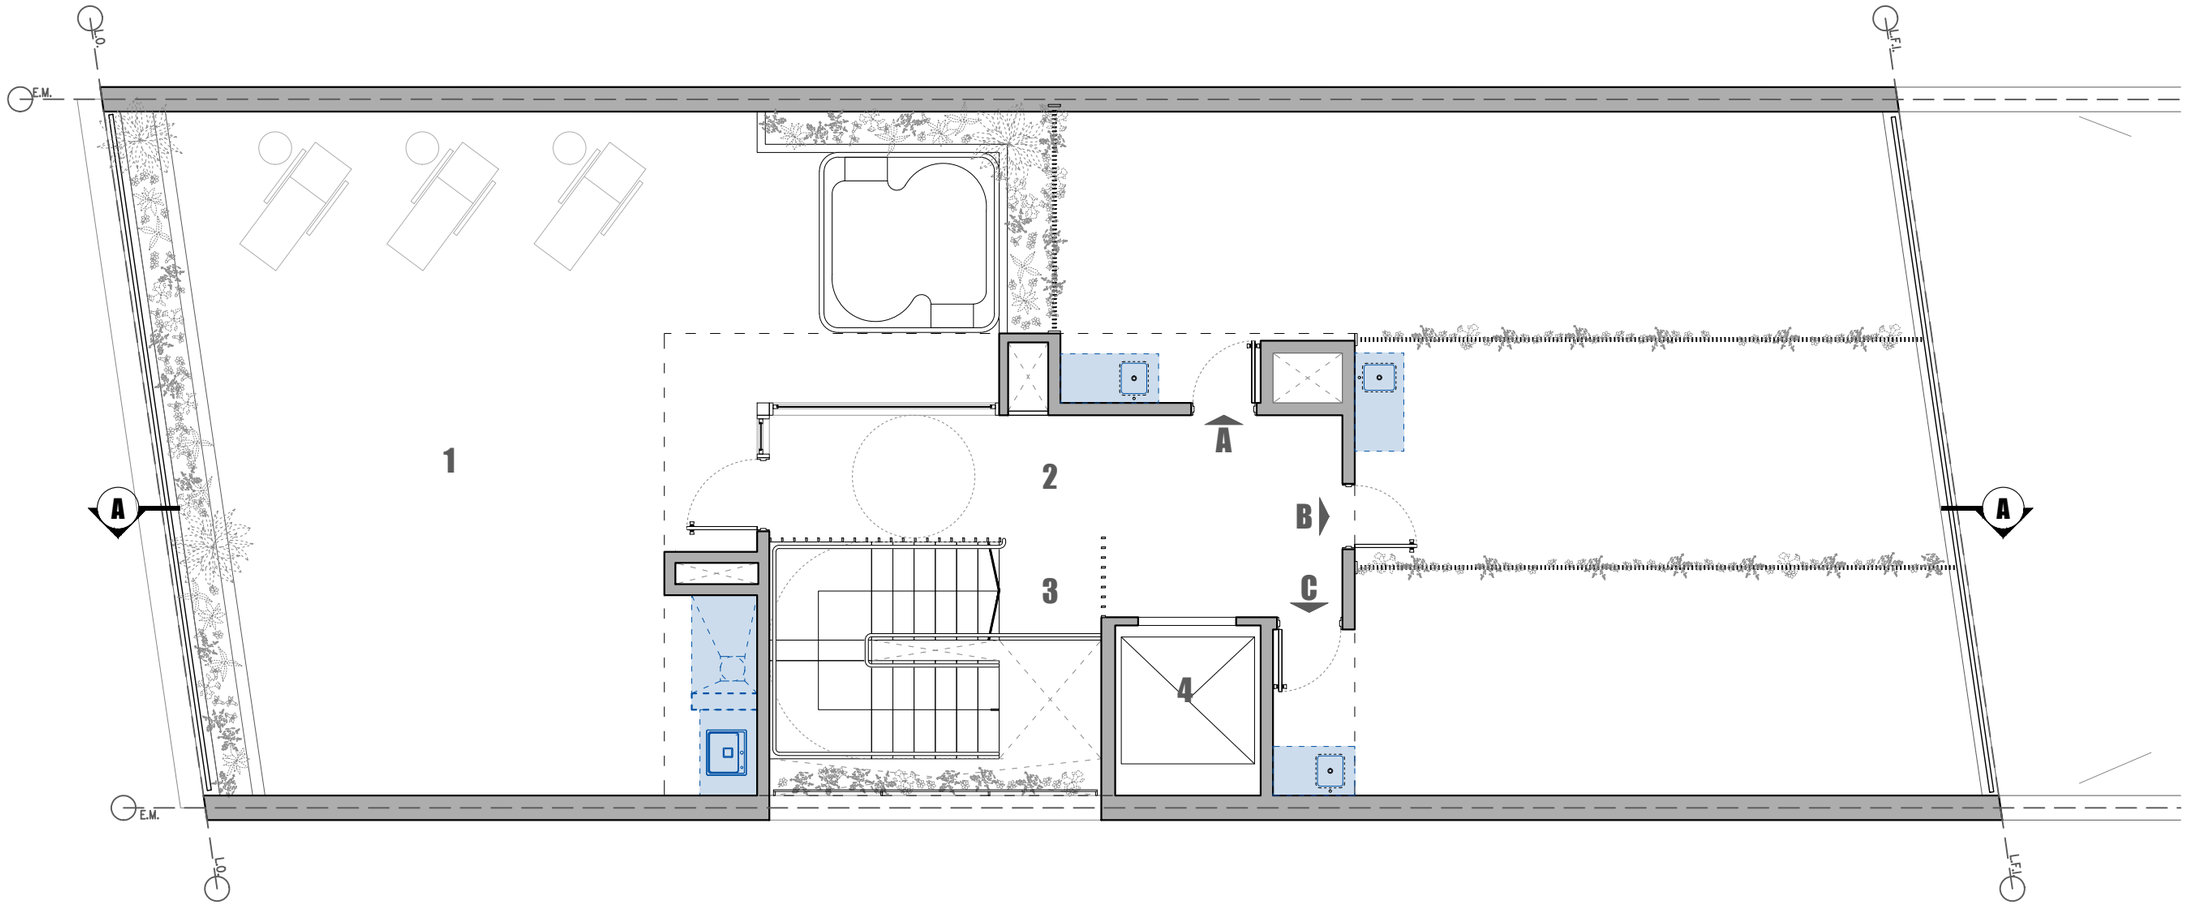

NOTA:
ELEMENTOS EN AZUL SON INTERVENCIONES POSTERIORES AL FINAL DE OBRA

REFERENCIAS

1. TERRAZA DE USO COMÚN
2. PALIER
3. ESCALERA
4. ASCENSOR


A. TERRAZA PRIVADA A
B. TERRAZA PRIVADA B
C. TERRAZA PRIVADA D

SUPERFICIES

- TERRAZA COMÚN: 76.30m²
- TERRAZA A: 33.11m²
- TERRAZA B: 20.45m²
- TERRAZA C: 24.86m²
- CIRCULACIONES: 32.77m²

CORTE A-A

ESC. 1:75

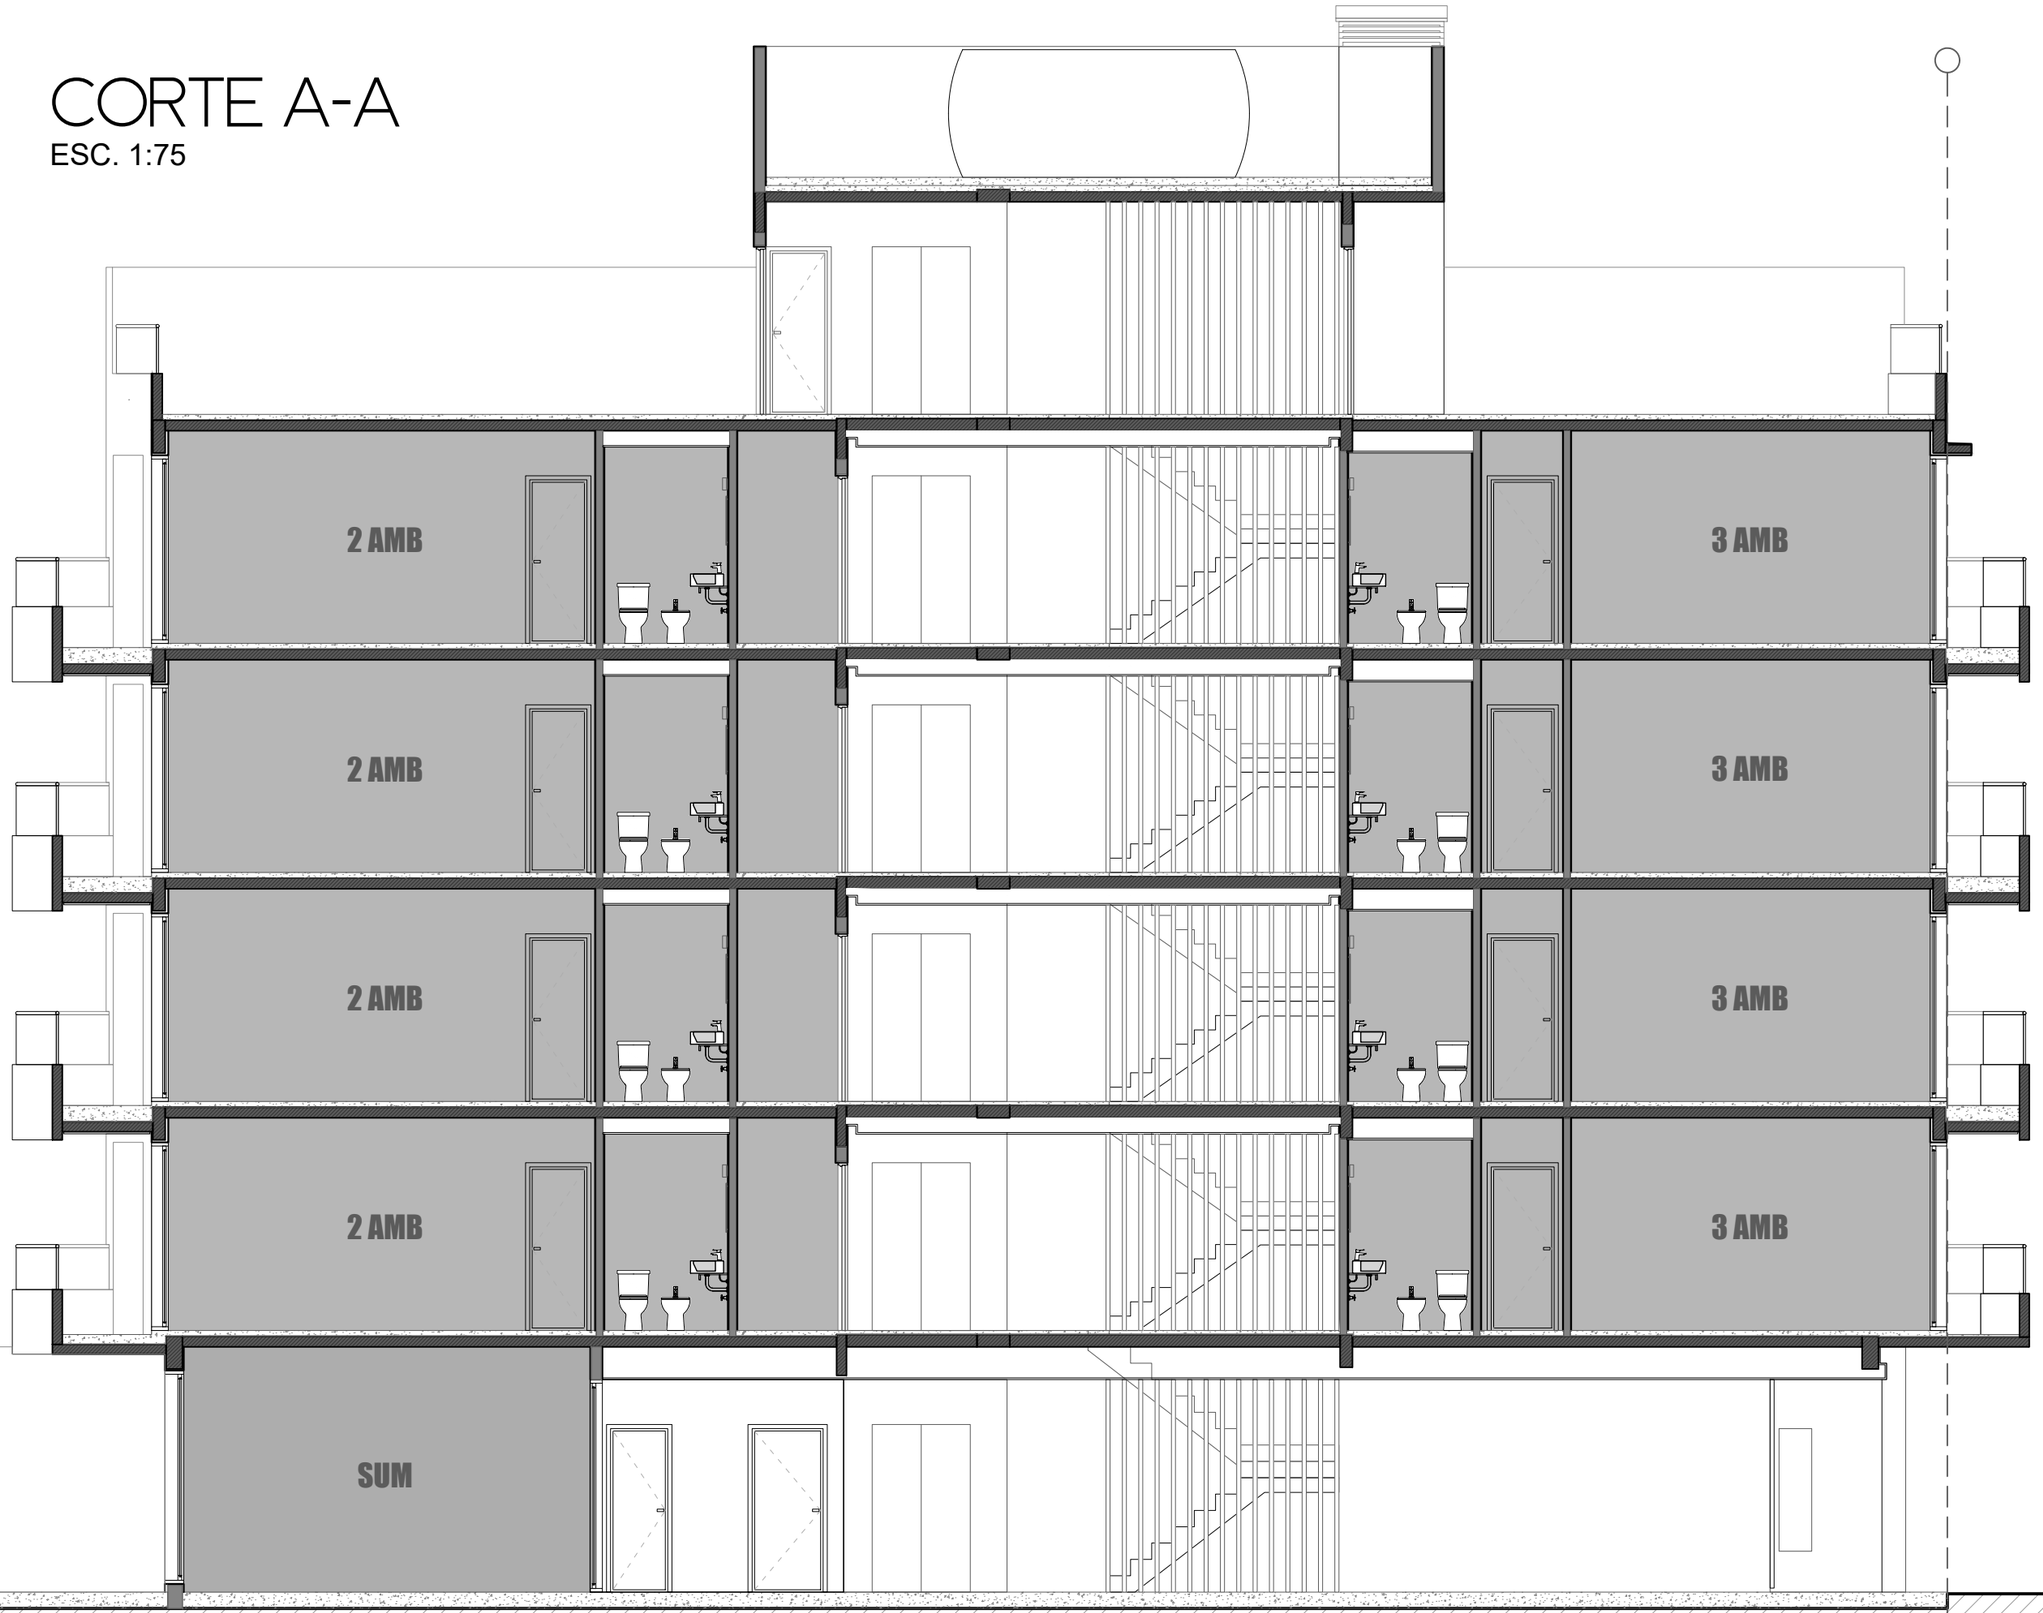

VIDAL 3849

SCHRAIFER GOLDIN ARQUITECTOS


3 AMBIENTES ESC. 1:50

DEPARTAMENTO A

CUBIERTO: 71.36 m^2
BALCÓN: 11.07 m^2
TOTAL: 82.43m^2



TERRAZA		
4A	4B	4C
3A	3B	3C
2A	2B	2C
1A	1B	1C
PLANTA BAJA		

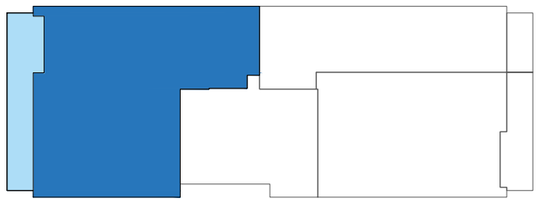


PLANTA TIPO


MONOAMBIENTE ESC. 1:50

DEPARTAMENTO B

CUBIERTO: 33.61 m^2
BALCÓN: 3.32 m^2
TOTAL: 36.93 m^2

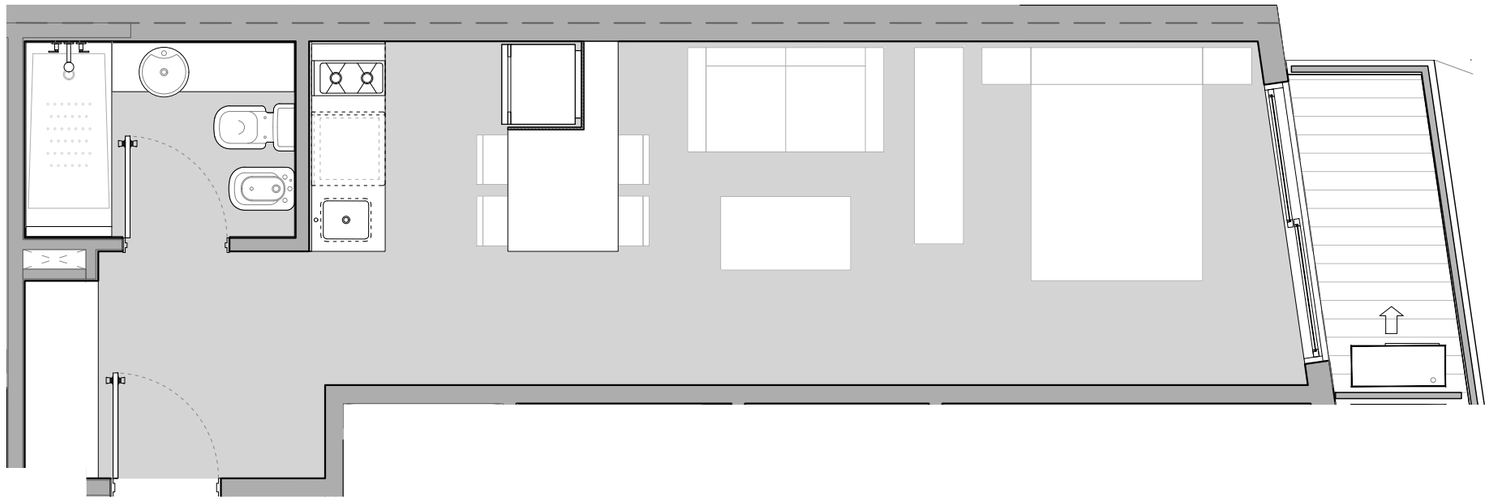


TERRAZA		
4A	4B	4C
3A	3B	3C
2A	2B	2C
1A	1B	1C
PLANTA BAJA		

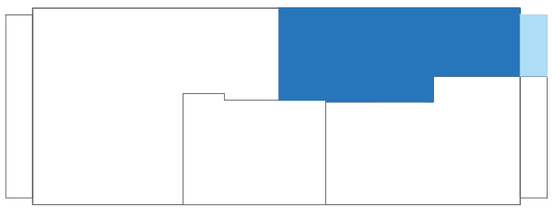


PLANTA TIPO

2 AMBIENTES ESC. 1:50

DEPARTAMENTO C
CUBIERTO: 47.81 m^2
BALCÓN: 6.46 m^2
TOTAL: 54.27m^2

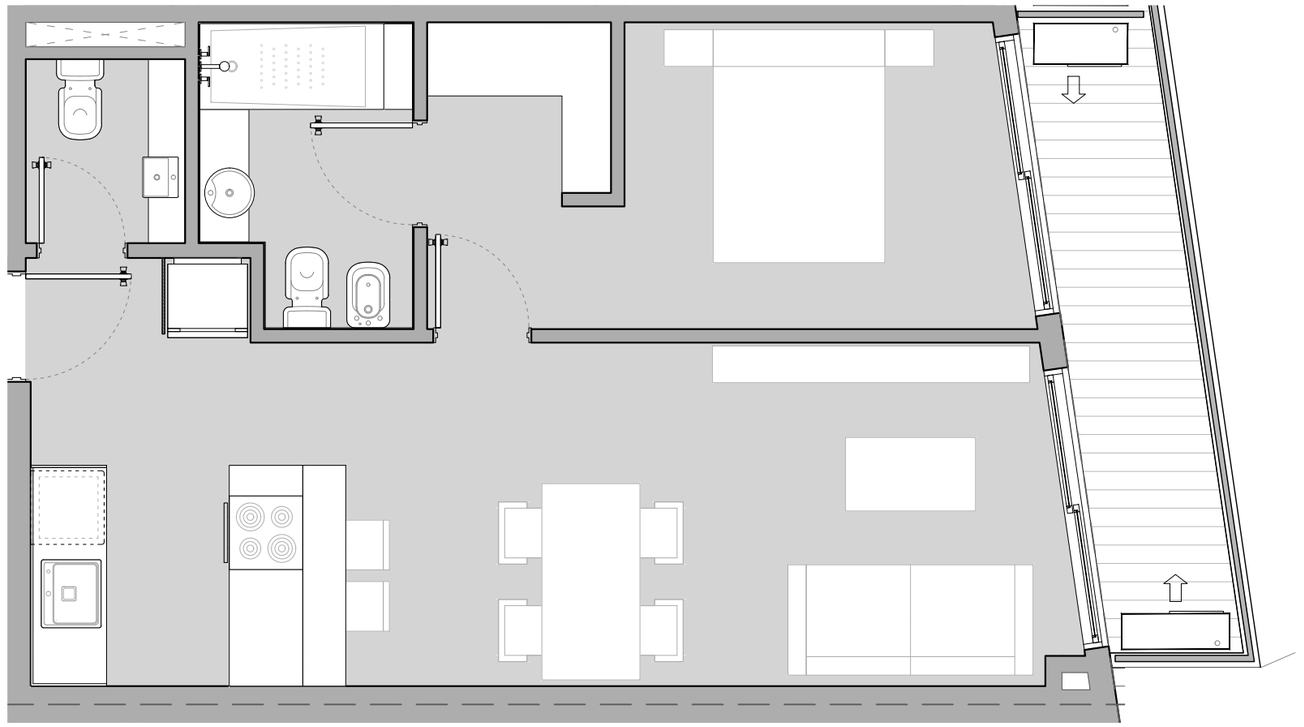

TERRAZA		
4A	4B	4C
3A	3B	3C
2A	2B	2C
1A	1B	1C
PLANTA BAJA		

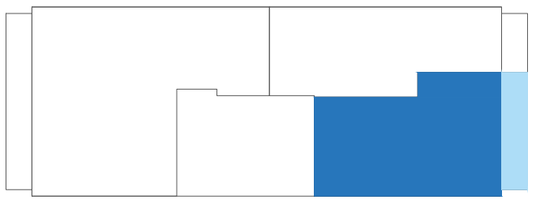

PLANTA TIPO